

# BAR ASSOCIATION HALL

## DISTRICT COURT COMPLEX, BANSWARA, RAJASTHAN

COMPREHENSIVE ARCHITECTURAL & STRUCTURAL REVIEW SET · G+1 BUILDING

|               |                                                    |
|---------------|----------------------------------------------------|
| PROJECT       | Bar Association Hall, Banswara                     |
| LOCATION      | District Court Complex, Banswara, Rajasthan, India |
| BUILDING TYPE | Bar Association Hall — G+1 (Ground + First Floor)  |
| PLANNING AREA | 4,427.50 sq.ft. per floor (Setback Envelope)       |
| MAIN ENTRANCE | East Long Wall — 12'-0" × 8'-0" Covered Porch      |
| FENESTRATION  | All Four Facades (North, South, East, West)        |
| STRUCTURE     | RCC Framed — IS 456:2000 / IS 1893:2016            |
| SCALE         | 1/8" = 1'-0"   Sheet: A2 Landscape                 |
| DATE          | 18-SEP-2026                                        |
| REVISION      | P01 — Approved Schematic                           |
| STATUS        | APPROVED SCHEMATIC DESIGN — NOT FOR CONSTRUCTION   |


### SHEET INDEX

| A-101                                      | A-201                                     | S-101                                   | A-102                                     | A-202                                    | S-102                                  |
|--------------------------------------------|-------------------------------------------|-----------------------------------------|-------------------------------------------|------------------------------------------|----------------------------------------|
| GROUND FLOOR PLAN<br>GF<br>BARE / NO FURN. | GROUND FLOOR PLAN<br>GF<br>WITH FURNITURE | GROUND FLOOR PLAN<br>GF<br>WITH COLUMNS | FIRST FLOOR PLAN<br>FF<br>BARE / NO FURN. | FIRST FLOOR PLAN<br>FF<br>WITH FURNITURE | FIRST FLOOR PLAN<br>FF<br>WITH COLUMNS |

# A-101 | GROUND FLOOR PLAN

ARCHITECTURAL FLOOR PLAN (WITHOUT FURNITURE)

BANSWARA DISTRICT COURT COMPLEX · COORDINATED ARCHITECTURAL SCHEMATIC

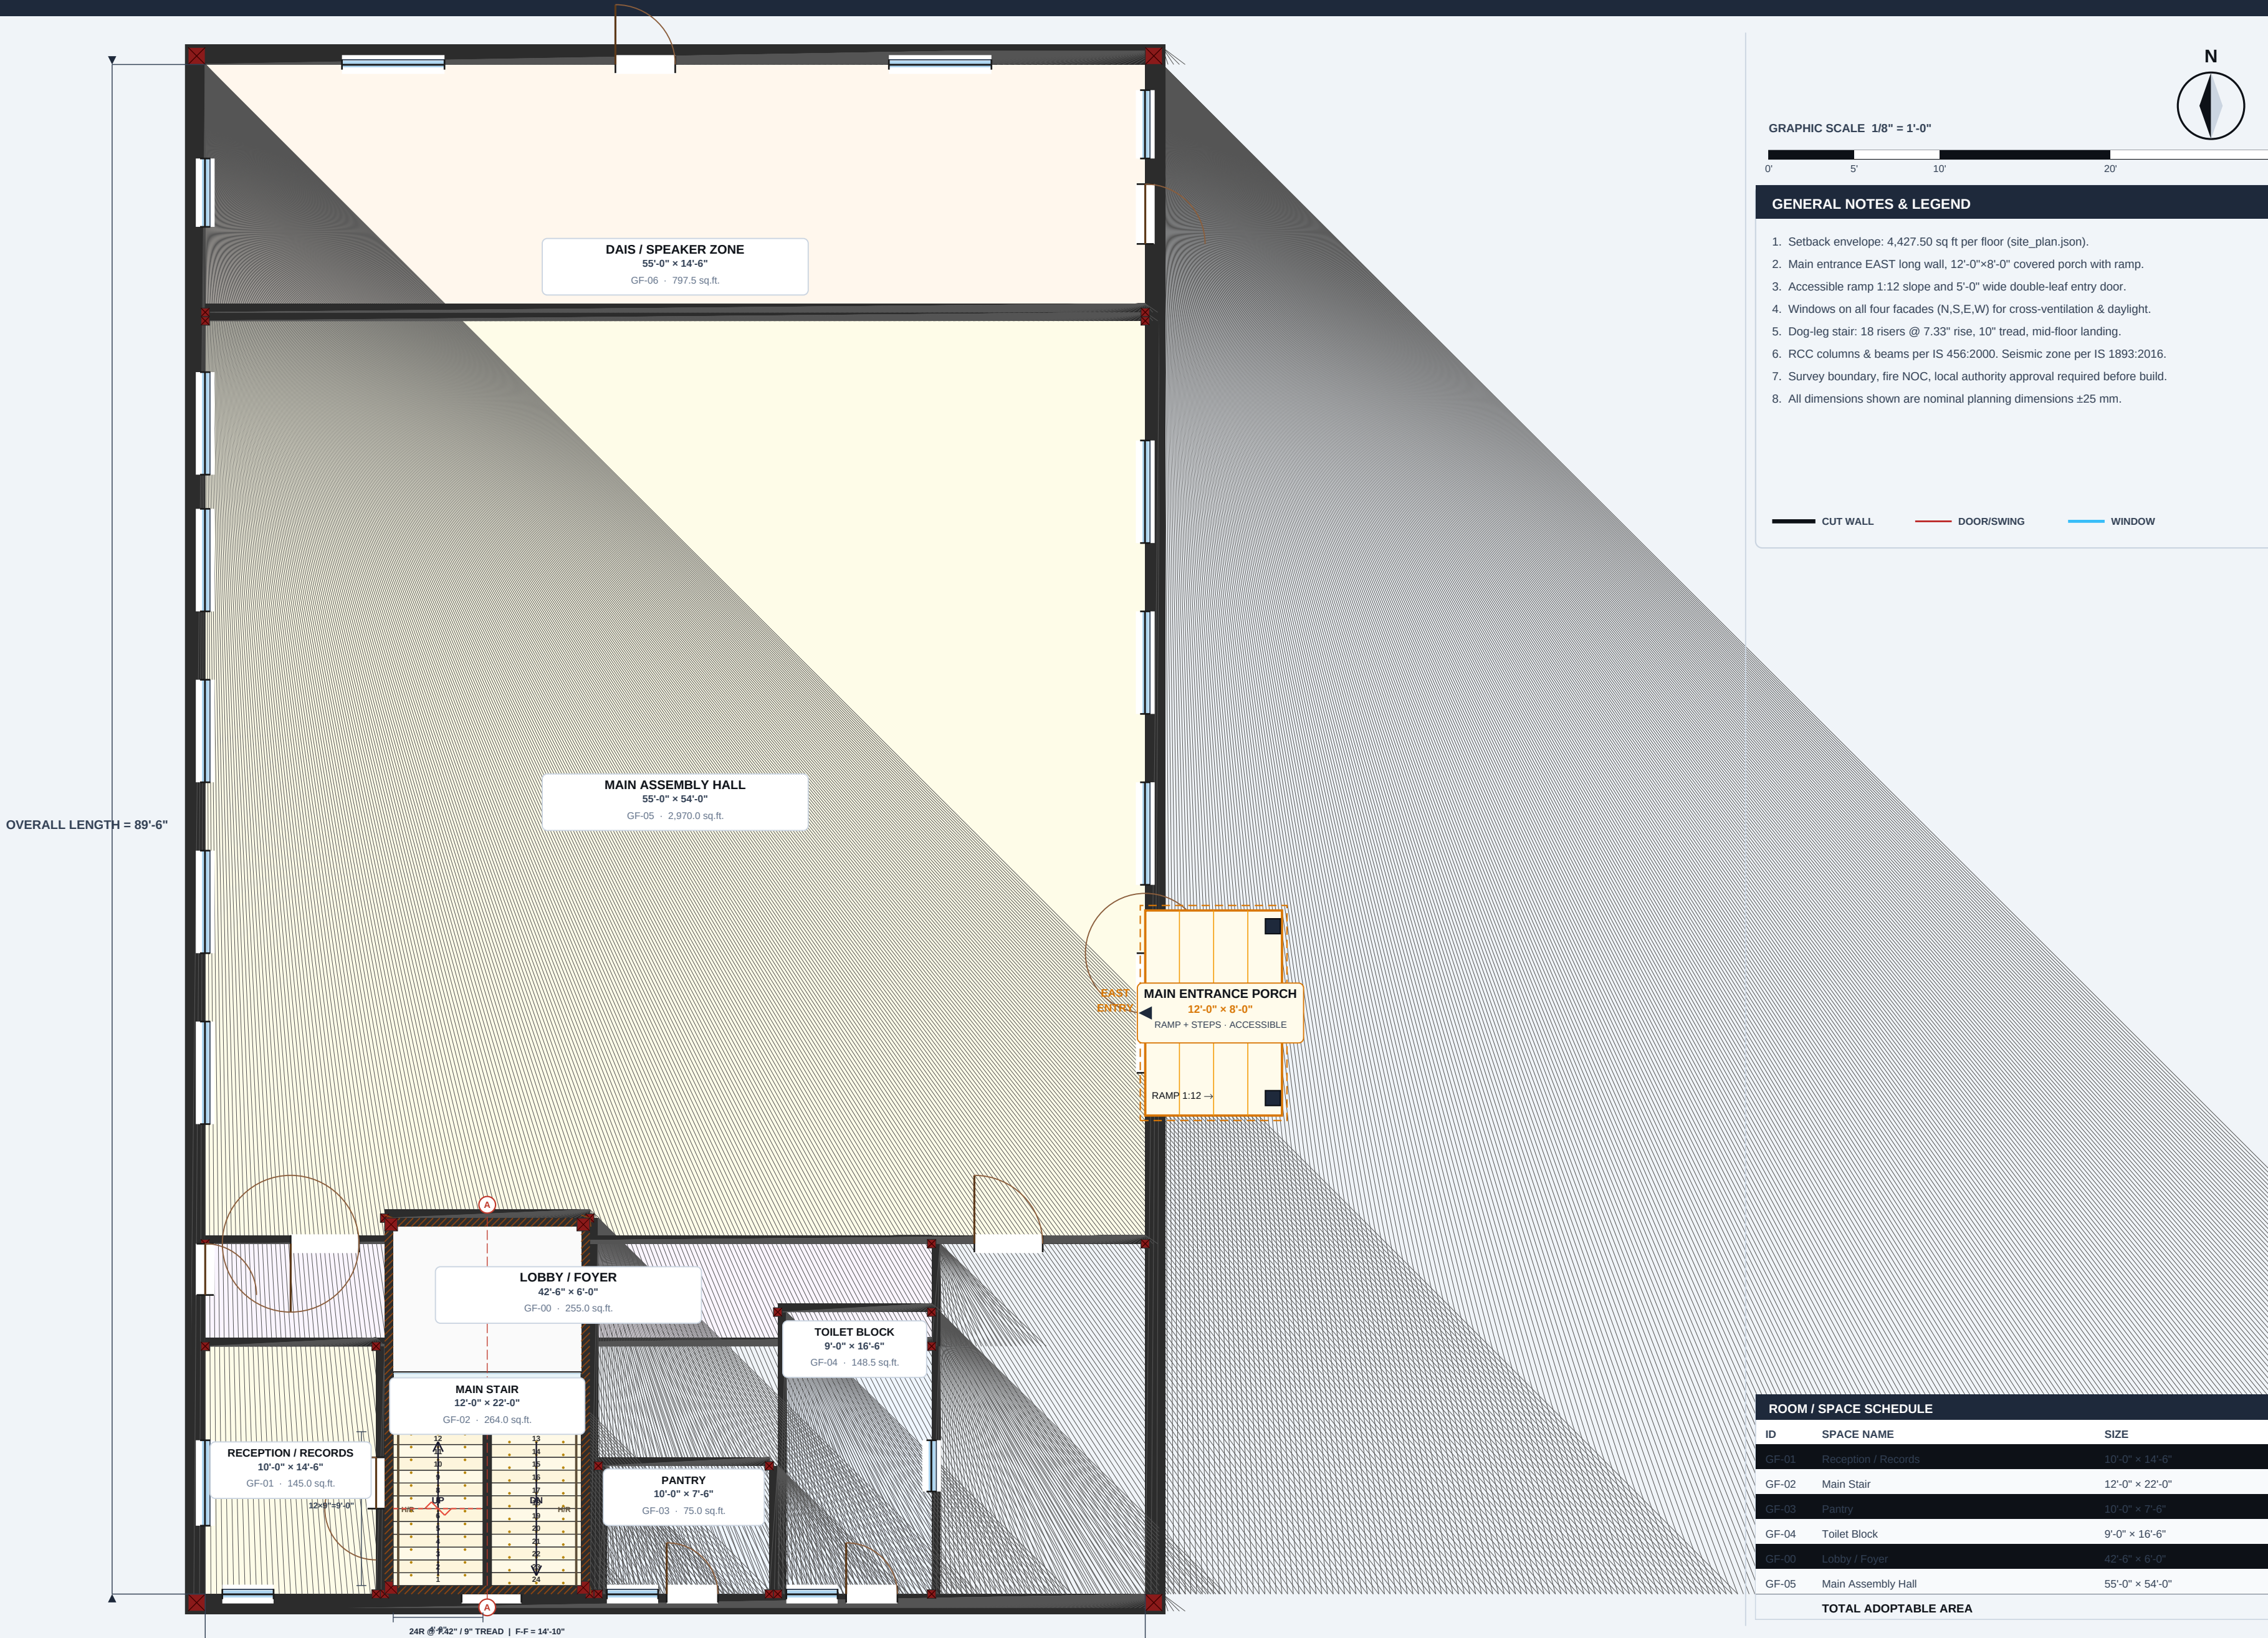

GRAPHIC SCALE 1/8" = 1'-0"

## GENERAL NOTES & LEGEND

- Setback envelope: 4,427.50 sq ft per floor (site\_plan.json).
- Main entrance EAST long wall, 12'-0"x8'-0" covered porch with ramp.
- Accessible ramp 1:12 slope and 5'-0" wide double-leaf entry door.
- Windows on all four facades (N,S,E,W) for cross-ventilation & daylight.
- Dog-leg stair: 18 risers @ 7.33" rise, 10" tread, mid-floor landing.
- RCC columns & beams per IS 456:2000. Seismic zone per IS 1893:2016.
- Survey boundary, fire NOC, local authority approval required before build.
- All dimensions shown are nominal planning dimensions ±25 mm.

CUT WALL DOOR/SWING WINDOW

## ROOM / SPACE SCHEDULE

| ID    | SPACE NAME          | SIZE            |
|-------|---------------------|-----------------|
| GF-01 | Reception / Records | 10'-0" x 14'-6" |
| GF-02 | Main Stair          | 12'-0" x 22'-0" |
| GF-03 | Pantry              | 10'-0" x 7'-6"  |
| GF-04 | Toilet Block        | 9'-0" x 16'-6"  |
| GF-00 | Lobby / Foyer       | 42'-6" x 6'-0"  |
| GF-05 | Main Assembly Hall  | 55'-0" x 54'-0" |

TOTAL ADOPTABLE AREA

BAR ASSOCIATION HALL  
DISTRICT COURT COMPLEX, BANSWARA  
RAJASTHAN, INDIA

PLANNING SETBACK ENVELOPE: 4,427.50 SQ.FT. PER FLOOR  
MAIN ENTRY: EAST LONG WALL · WINDOWS: ALL FOUR SIDES

GROUND FLOOR PLAN  
ARCHITECTURAL FLOOR PLAN (WITHOUT FURNITURE)  
LEVEL: GROUND FLOOR SCALE: 1/8" = 1'-0" (A2 LANDSCAPE)

STRUCTURE: RCC FRAME IS 456:2000 / IS 1893:2016  
STATUS: APPROVED SCHEMATIC — NOT FOR CONSTRUCTION

A-101


SHEET NO.

REV: P01  
18-SEP-2026

# A-201 | GROUND FLOOR PLAN

PRESENTATION FLOOR PLAN (WITH FURNITURE)

BANSWARA DISTRICT COURT COMPLEX · COORDINATED ARCHITECTURAL SCHEMATIC

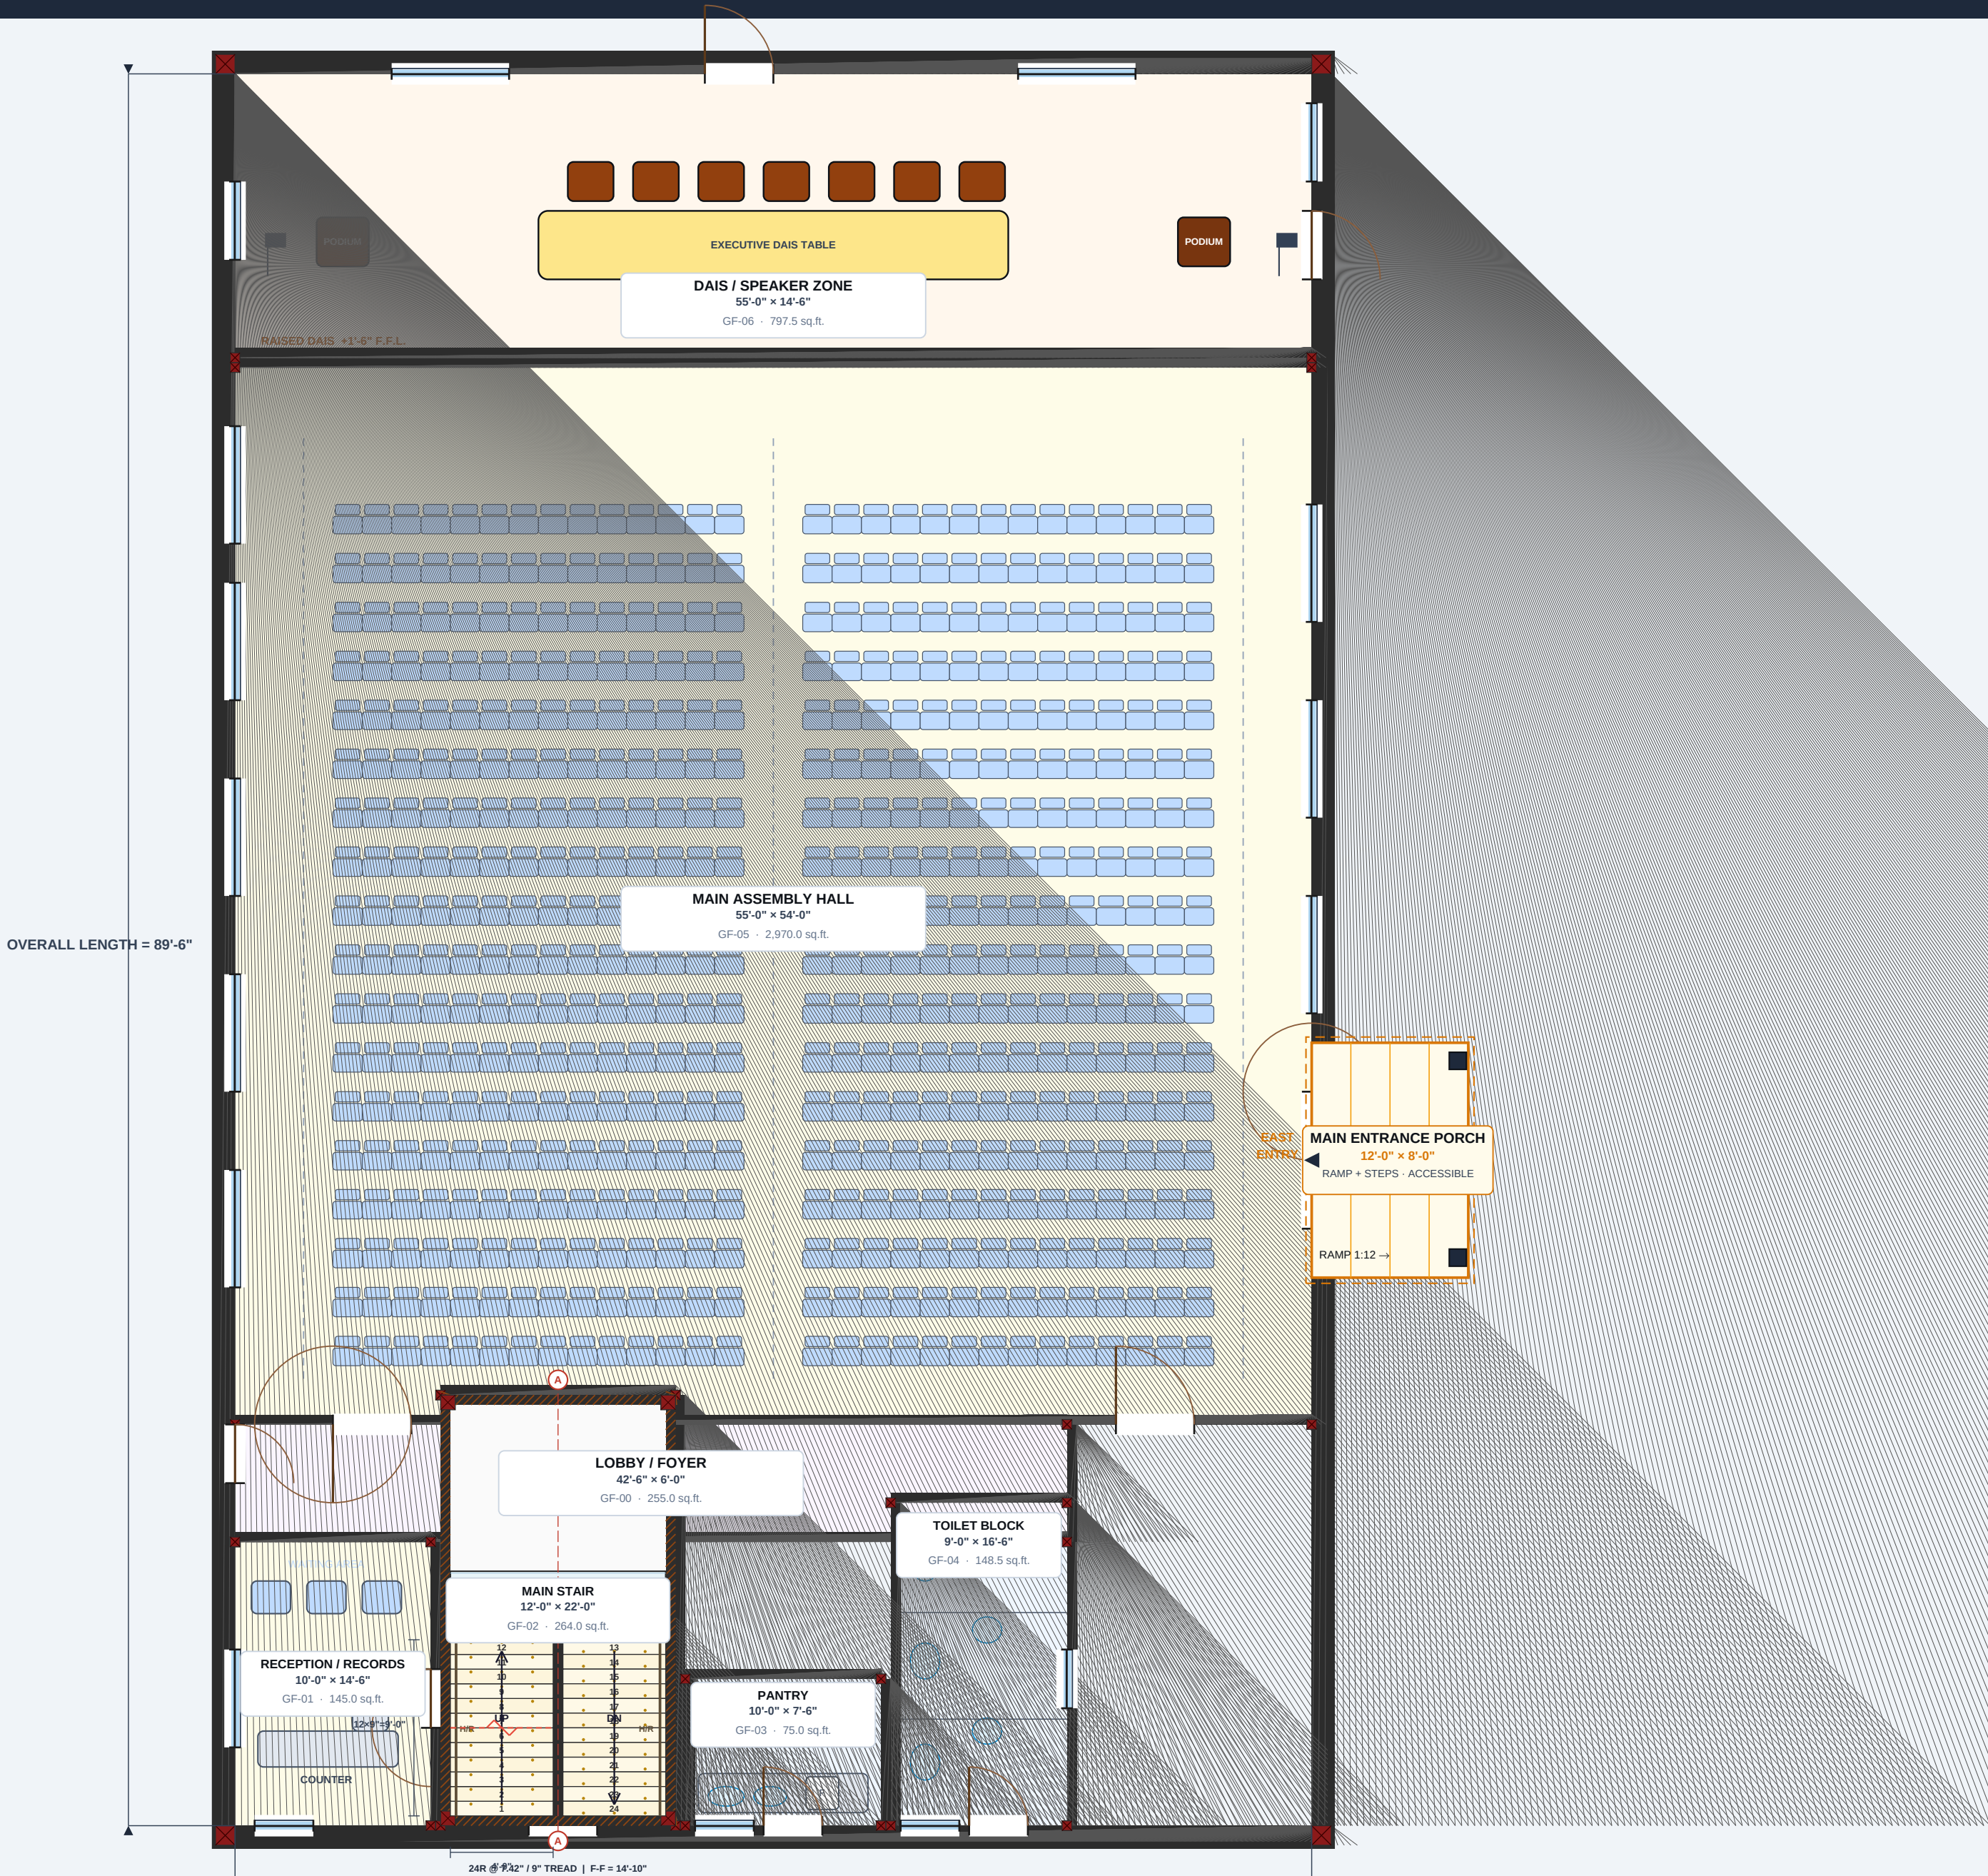

GRAPHIC SCALE 1/8" = 1'-0"

## GENERAL NOTES & LEGEND

- Setback envelope: 4,427.50 sq ft per floor (site\_plan.json).
- Main entrance EAST long wall, 12'-0"x8'-0" covered porch with ramp.
- Accessible ramp 1:12 slope and 5'-0" wide double-leaf entry door.
- Windows on all four facades (N,S,E,W) for cross-ventilation & daylight.
- Dog-leg stair: 18 risers @ 7.33" rise, 10" tread, mid-floor landing.
- RCC columns & beams per IS 456:2000. Seismic zone per IS 1893:2016.
- Survey boundary, fire NOC, local authority approval required before build.
- All dimensions shown are nominal planning dimensions ±25 mm.

CUT WALL DOOR/SWING WINDOW FURNITURE

## ROOM / SPACE SCHEDULE

| ID                   | SPACE NAME          | SIZE            |
|----------------------|---------------------|-----------------|
| GF-01                | Reception / Records | 10'-0" x 14'-6" |
| GF-02                | Main Stair          | 12'-0" x 22'-0" |
| GF-03                | Pantry              | 10'-0" x 7'-6"  |
| GF-04                | Toilet Block        | 9'-0" x 16'-6"  |
| GF-00                | Lobby / Foyer       | 42'-6" x 6'-0"  |
| GF-05                | Main Assembly Hall  | 55'-0" x 54'-0" |
| TOTAL ADOPTABLE AREA |                     |                 |

BAR ASSOCIATION HALL  
DISTRICT COURT COMPLEX, BANSWARA  
RAJASTHAN, INDIA

PLANNING SETBACK ENVELOPE: 4,427.50 SQ.FT. PER FLOOR  
MAIN ENTRY: EAST LONG WALL · WINDOWS: ALL FOUR SIDES

## GROUND FLOOR PLAN

PRESENTATION FLOOR PLAN (WITH FURNITURE)

LEVEL: GROUND FLOOR SCALE: 1/8" = 1'-0" (A2 LANDSCAPE)

STRUCTURE: RCC FRAME IS 456:2000 / IS 1893:2016

STATUS: APPROVED SCHEMATIC — NOT FOR CONSTRUCTION

A-201


SHEET NO.

REV: P01  
18-SEP-2026

# S-101 | GROUND FLOOR PLAN

STRUCTURAL COLUMN & GRID COORDINATION PLAN (WITH COLUMNS)

BANSWARA DISTRICT COURT COMPLEX · COORDINATED ARCHITECTURAL SCHEMATIC

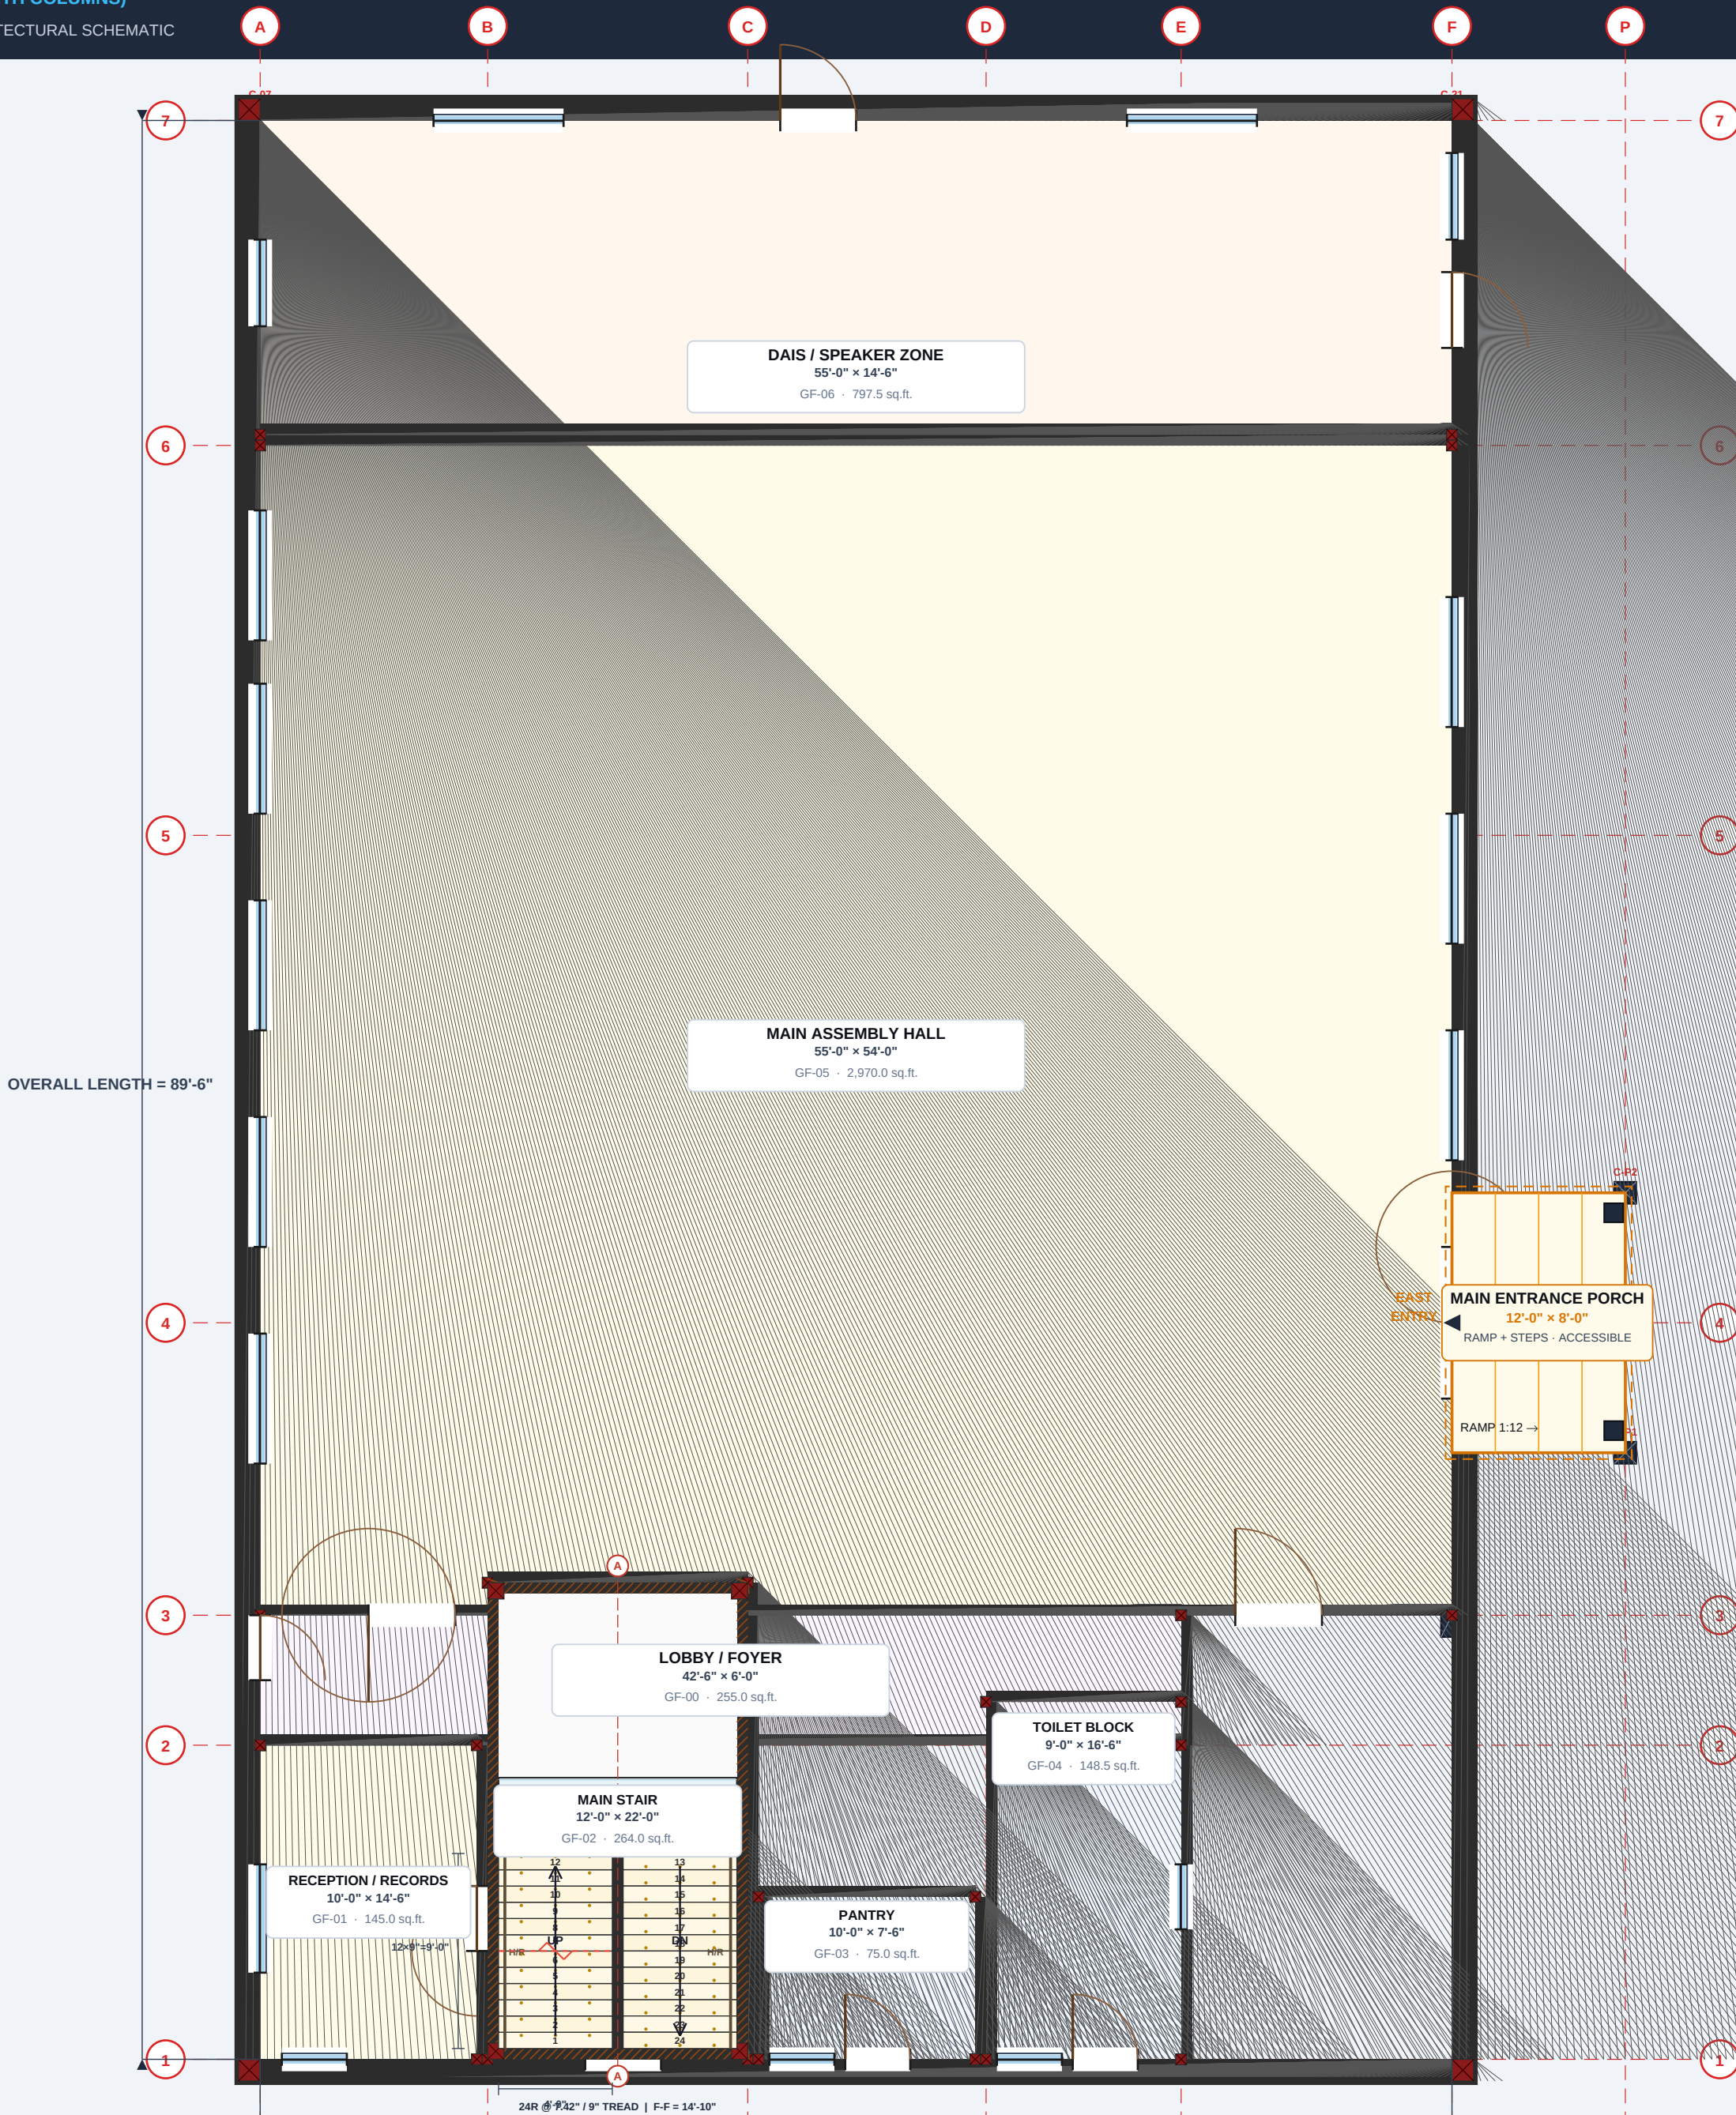

GRAPHIC SCALE 1/8" = 1'-0"

## GENERAL NOTES & LEGEND

- Setback envelope: 4,427.50 sq ft per floor (site\_plan.json).
- Main entrance EAST long wall, 12'-0"x8'-0" covered porch with ramp.
- Accessible ramp 1:12 slope and 5'-0" wide double-leaf entry door.
- Windows on all four facades (N,S,E,W) for cross-ventilation & daylight.
- Dog-leg stair: 18 risers @ 7.33" rise, 10" tread, mid-floor landing.
- RCC columns & beams per IS 456:2000. Seismic zone per IS 1893:2016.
- Survey boundary, fire NOC, local authority approval required before build.
- All dimensions shown are nominal planning dimensions ±25 mm.

CUT WALL DOOR/SWING WINDOW RCC COLUMN

## STRUCTURAL COLUMN SCHEDULE

| MARK / SIZE    | MAIN REBAR                | ZONE                          |
|----------------|---------------------------|-------------------------------|
| C1 - 300x600mm | 8-T20+4-T16, Links T8@150 | Main hall long-span perimeter |
| C2 - 300x450mm | 8-T16, Links T8@150       | Service core, stair, dais     |
| CP - 300x300mm | 4-T16, Links T8@150       | Entrance porch canopy posts   |

M25 CONCRETE | Fe500D STEEL | ISOLATED RCC FOOTINGS

BAR ASSOCIATION HALL  
DISTRICT COURT COMPLEX, BANSWARA  
RAJASTHAN, INDIA

PLANNING SETBACK ENVELOPE: 4,427.50 SQ.FT. PER FLOOR  
MAIN ENTRY: EAST LONG WALL · WINDOWS: ALL FOUR SIDES

GROUND FLOOR PLAN  
STRUCTURAL COLUMN & GRID COORDINATION PLAN (WITH COLUMNS)  
LEVEL: GROUND FLOOR SCALE: 1/8" = 1'-0" (A2 LANDSCAPE)

STRUCTURE: RCC FRAME IS 456:2000 / IS 1893:2016  
STATUS: APPROVED SCHEMATIC — NOT FOR CONSTRUCTION

S-101


SHEET NO.

REV: P01  
18-SEP-2026

# A-102 | FIRST FLOOR PLAN

ARCHITECTURAL FLOOR PLAN (WITHOUT FURNITURE)

BANSWARA DISTRICT COURT COMPLEX · COORDINATED ARCHITECTURAL SCHEMATIC

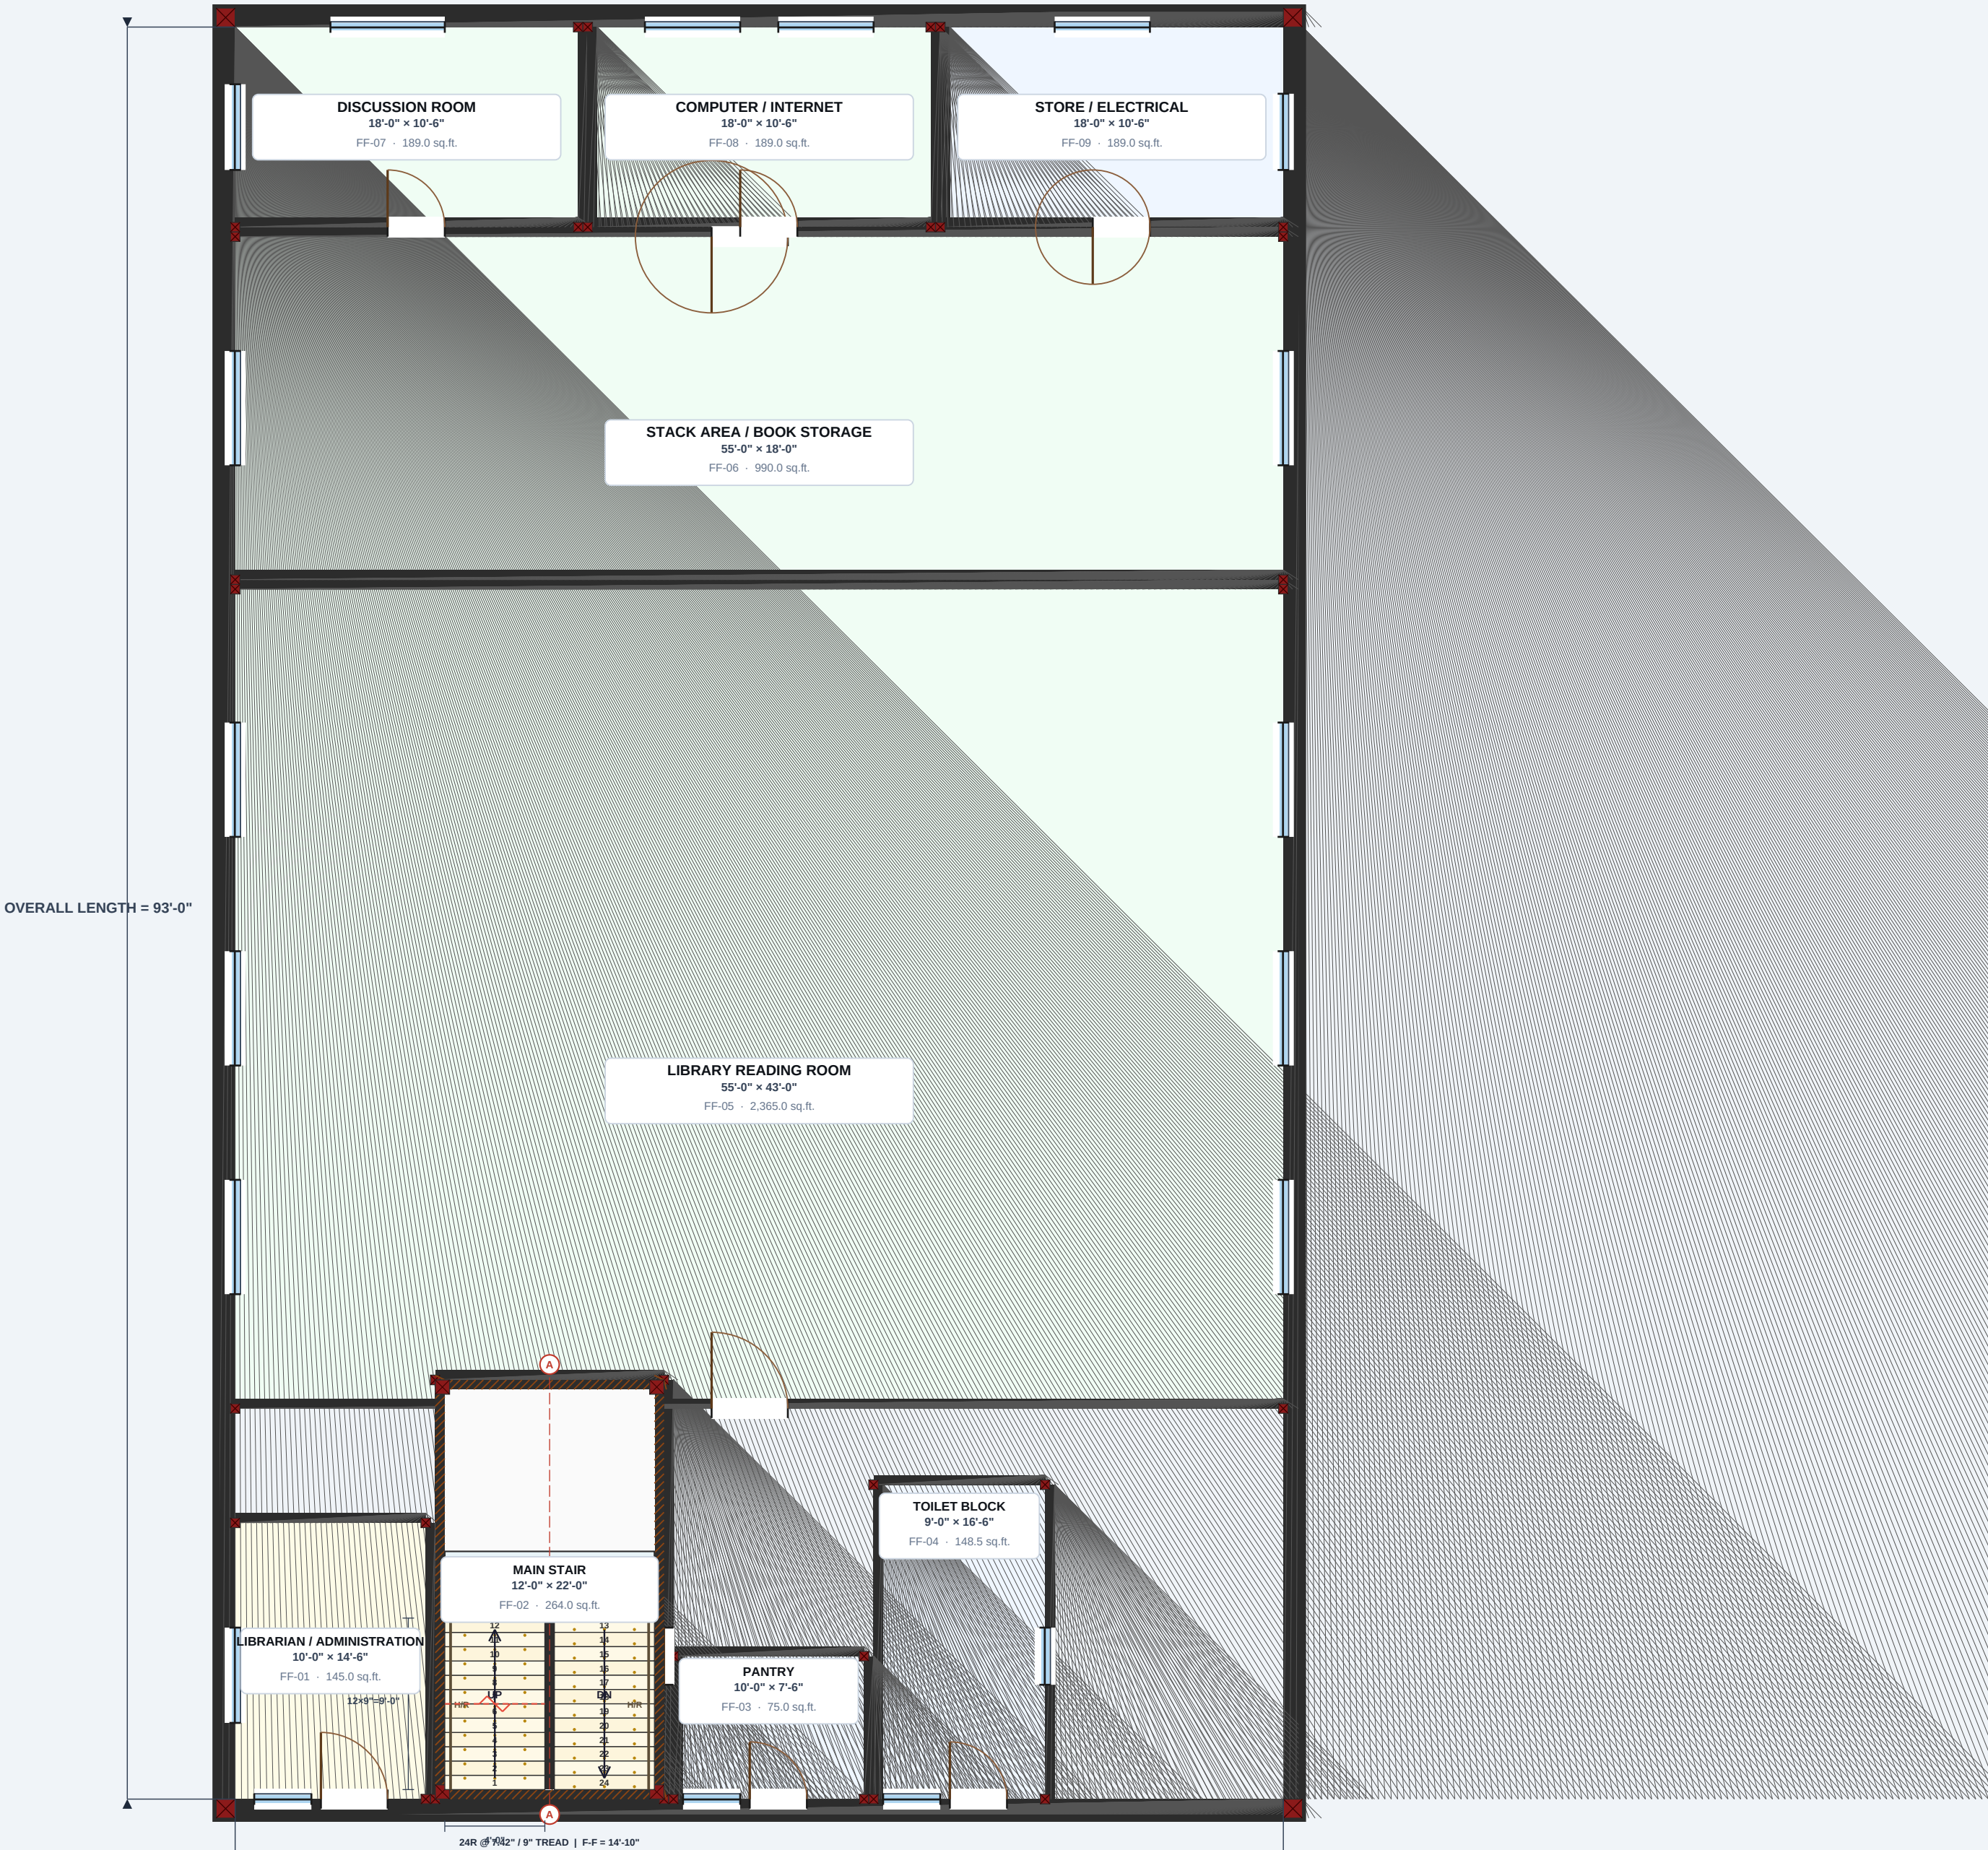

GRAPHIC SCALE 1/8" = 1'-0"

## GENERAL NOTES & LEGEND

- Setback envelope: 4,427.50 sq ft per floor (site\_plan.json).
- Main entrance EAST long wall, 12'-0"×8'-0" covered porch with ramp.
- Accessible ramp 1:12 slope and 5'-0" wide double-leaf entry door.
- Windows on all four facades (N,S,E,W) for cross-ventilation & daylight.
- Dog-leg stair: 18 risers @ 7.33" rise, 10" tread, mid-floor landing.
- RCC columns & beams per IS 456:2000. Seismic zone per IS 1893:2016.
- Survey boundary, fire NOC, local authority approval required before build.
- All dimensions shown are nominal planning dimensions ±25 mm.

CUT WALL DOOR/SWING WINDOW

## ROOM / SPACE SCHEDULE

| ID                   | SPACE NAME                 | SIZE            |
|----------------------|----------------------------|-----------------|
| FF-01                | Librarian / Administration | 10'-0" × 14'-6" |
| FF-02                | Main Stair                 | 12'-0" × 22'-0" |
| FF-03                | Pantry                     | 10'-0" × 7'-6"  |
| FF-04                | Toilet Block               | 9'-0" × 16'-6"  |
| FF-05                | Library Reading Room       | 55'-0" × 43'-0" |
| FF-06                | Stack Area / Book Storage  | 55'-0" × 18'-0" |
| FF-07                | Discussion Room            | 18'-0" × 10'-6" |
| FF-08                | Computer / Internet        | 18'-0" × 10'-6" |
| TOTAL ADOPTABLE AREA |                            |                 |

BAR ASSOCIATION HALL  
DISTRICT COURT COMPLEX, BANSWARA  
RAJASTHAN, INDIA

PLANNING SETBACK ENVELOPE: 4,427.50 SQ.FT. PER FLOOR  
MAIN ENTRY: EAST LONG WALL · WINDOWS: ALL FOUR SIDES

FIRST FLOOR PLAN  
ARCHITECTURAL FLOOR PLAN (WITHOUT FURNITURE)  
LEVEL: FIRST FLOOR SCALE: 1/8" = 1'-0" (A2 LANDSCAPE)

STRUCTURE: RCC FRAME IS 456:2000 / IS 1893:2016  
STATUS: APPROVED SCHEMATIC — NOT FOR CONSTRUCTION

A-102


SHEET NO.

REV: P01  
18-SEP-2026

A-202 | FIRST FLOOR PLAN

PRESENTATION FLOOR PLAN (WITH FURNITURE)

BANSWARA DISTRICT COURT COMPLEX · COORDINATED ARCHITECTURAL SCHEMATIC

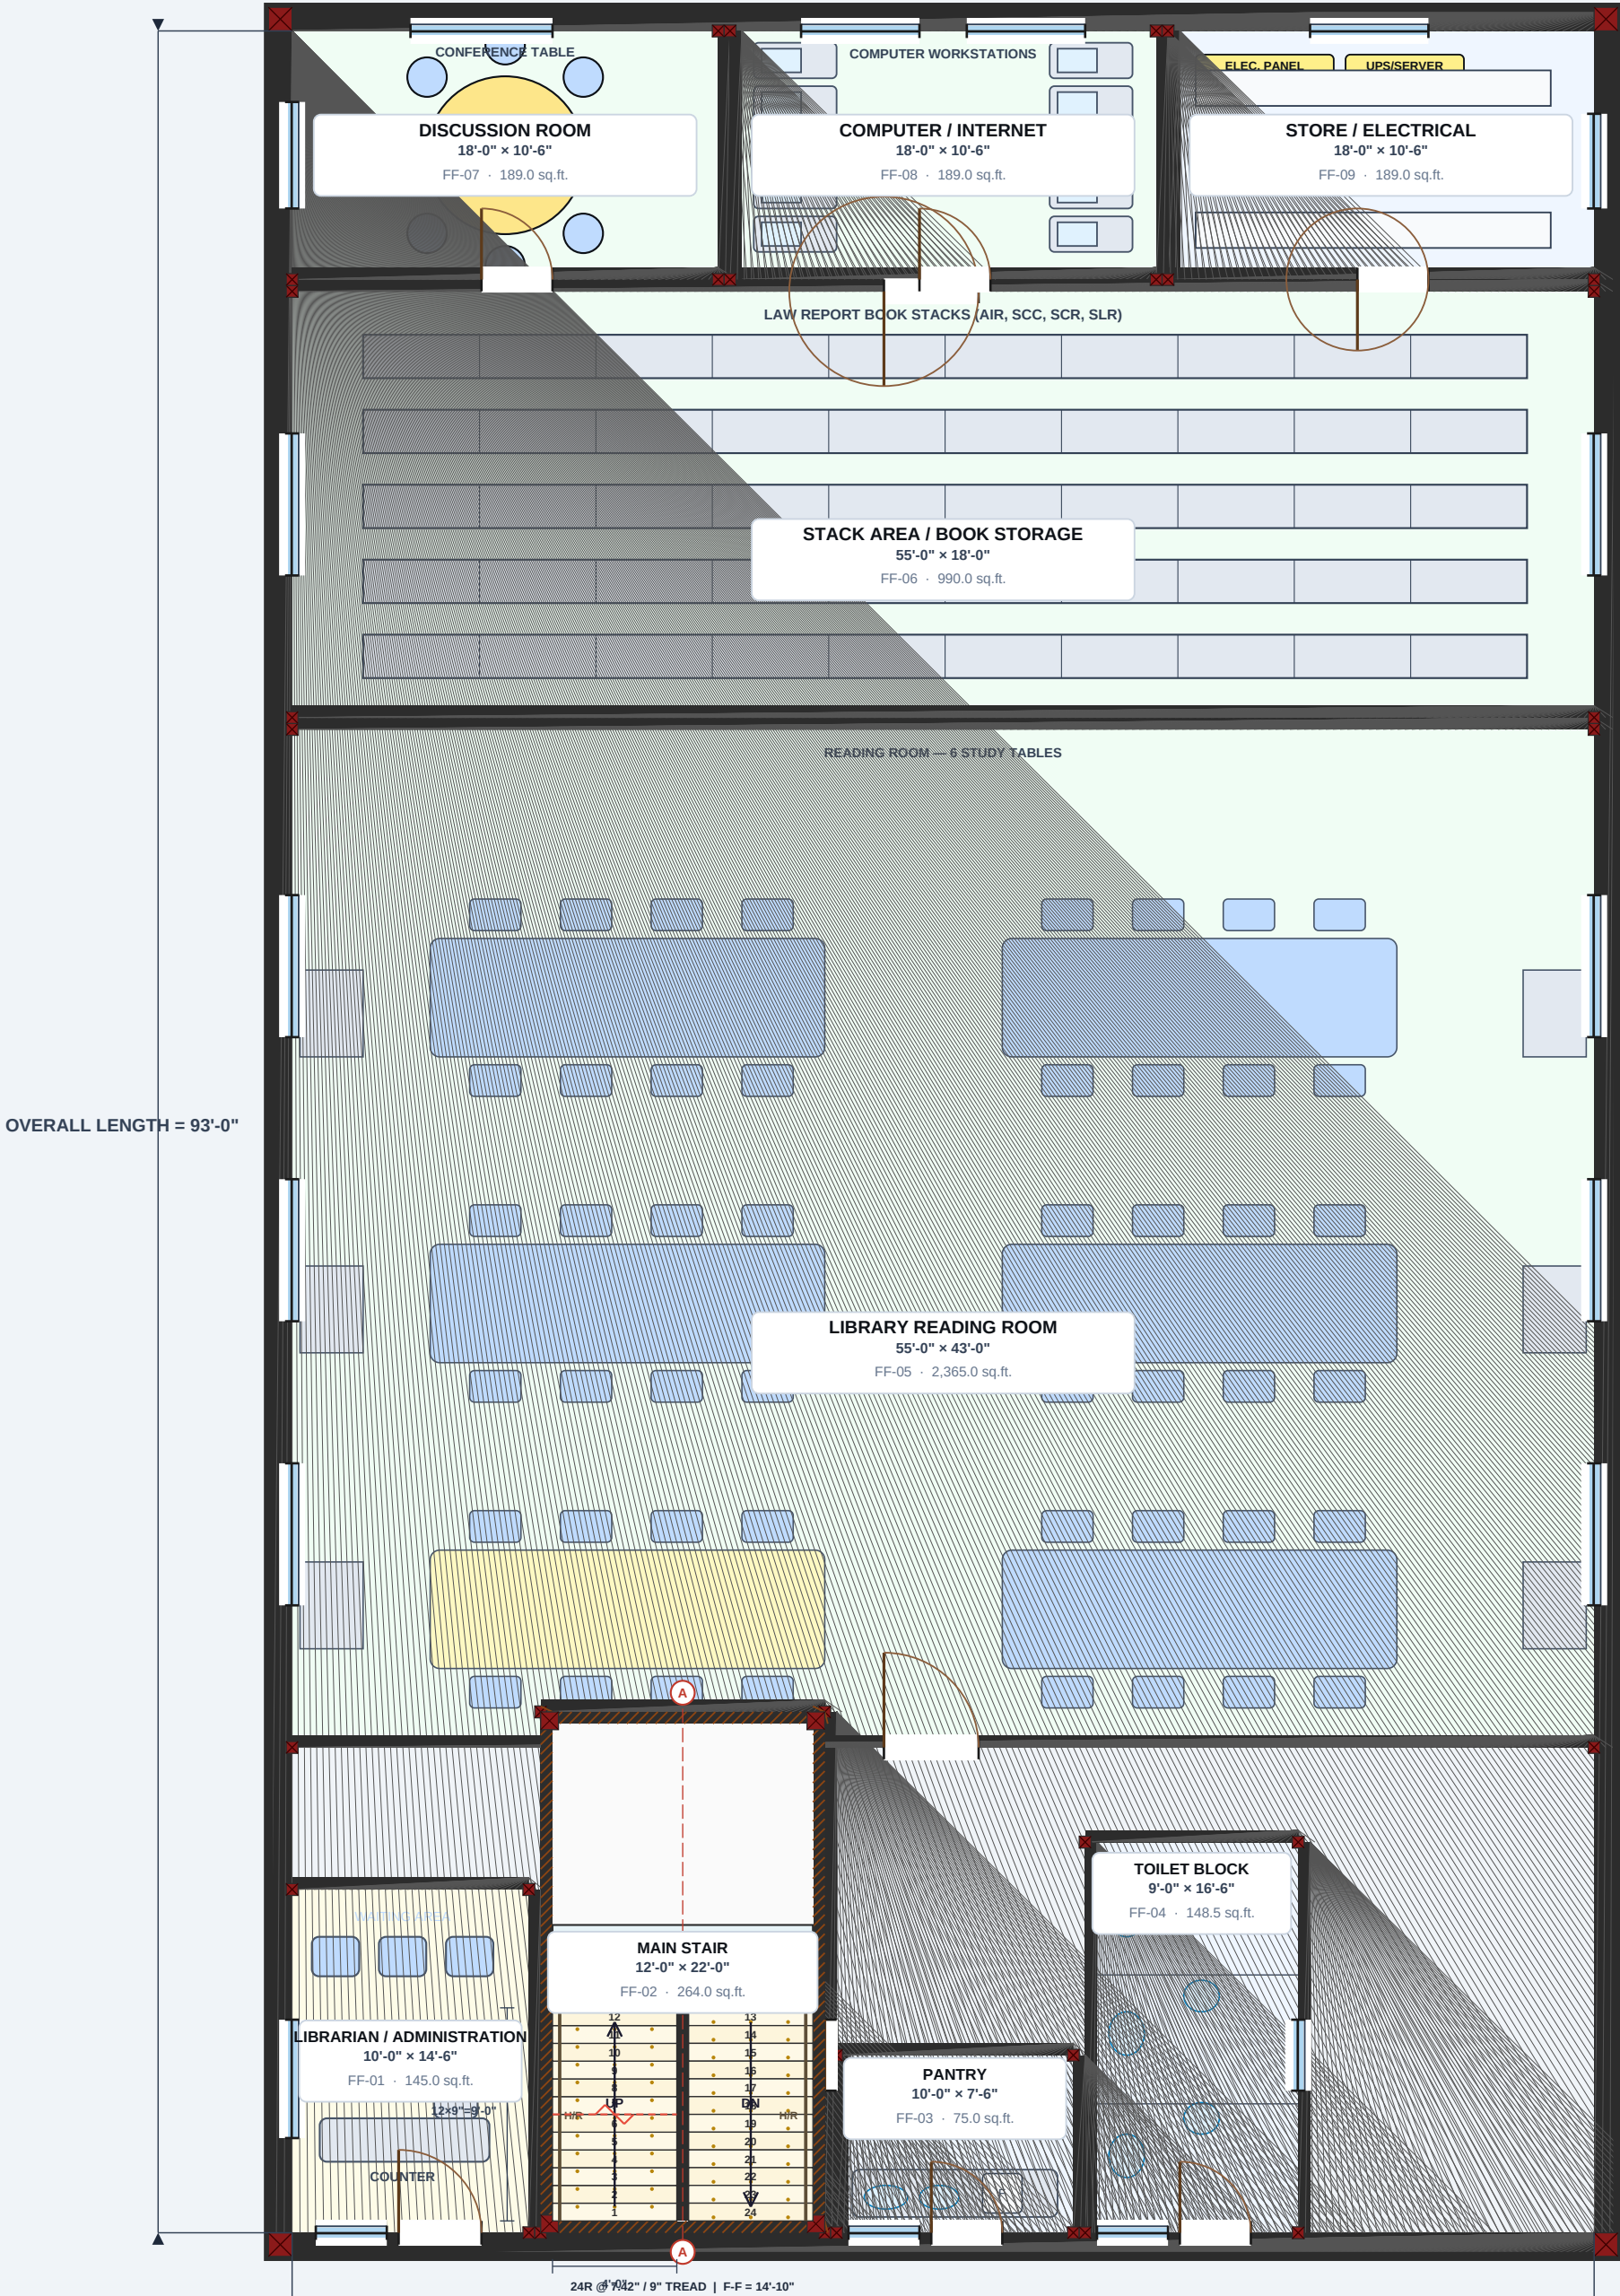

GRAPHIC SCALE 1/8" = 1'-0"

GENERAL NOTES & LEGEND

- Setback envelope: 4,427.50 sq ft per floor (site\_plan.json).
- Main entrance EAST long wall, 12'-0"×8'-0" covered porch with ramp.
- Accessible ramp 1:12 slope and 5'-0" wide double-leaf entry door.
- Windows on all four facades (N,S,E,W) for cross-ventilation & daylight.
- Dog-leg stair: 18 risers @ 7.33" rise, 10" tread, mid-floor landing.
- RCC columns & beams per IS 456:2000. Seismic zone per IS 1893:2016.
- Survey boundary, fire NOC, local authority approval required before build.
- All dimensions shown are nominal planning dimensions ±25 mm.

CUT WALL DOOR/SWING WINDOW FURNITURE

BAR ASSOCIATION HALL  
DISTRICT COURT COMPLEX, BANSWARA  
RAJASTHAN, INDIA

PLANNING SETBACK ENVELOPE: 4,427.50 SQ.FT. PER FLOOR  
MAIN ENTRY: EAST LONG WALL · WINDOWS: ALL FOUR SIDES


FIRST FLOOR PLAN  
PRESENTATION FLOOR PLAN (WITH FURNITURE)  
LEVEL: FIRST FLOOR SCALE: 1/8" = 1'-0" (A2 LANDSCAPE)  
STRUCTURE: RCC FRAME IS 456:2000 / IS 1893:2016  
STATUS: APPROVED SCHEMATIC — NOT FOR CONSTRUCTION

A-202  
SHEET NO.  
REV: P01  
18-SEP-2026

# S-102 | FIRST FLOOR PLAN

STRUCTURAL COLUMN & GRID COORDINATION PLAN (WITH COLUMNS)

BANSWARA DISTRICT COURT COMPLEX · COORDINATED ARCHITECTURAL SCHEMATIC

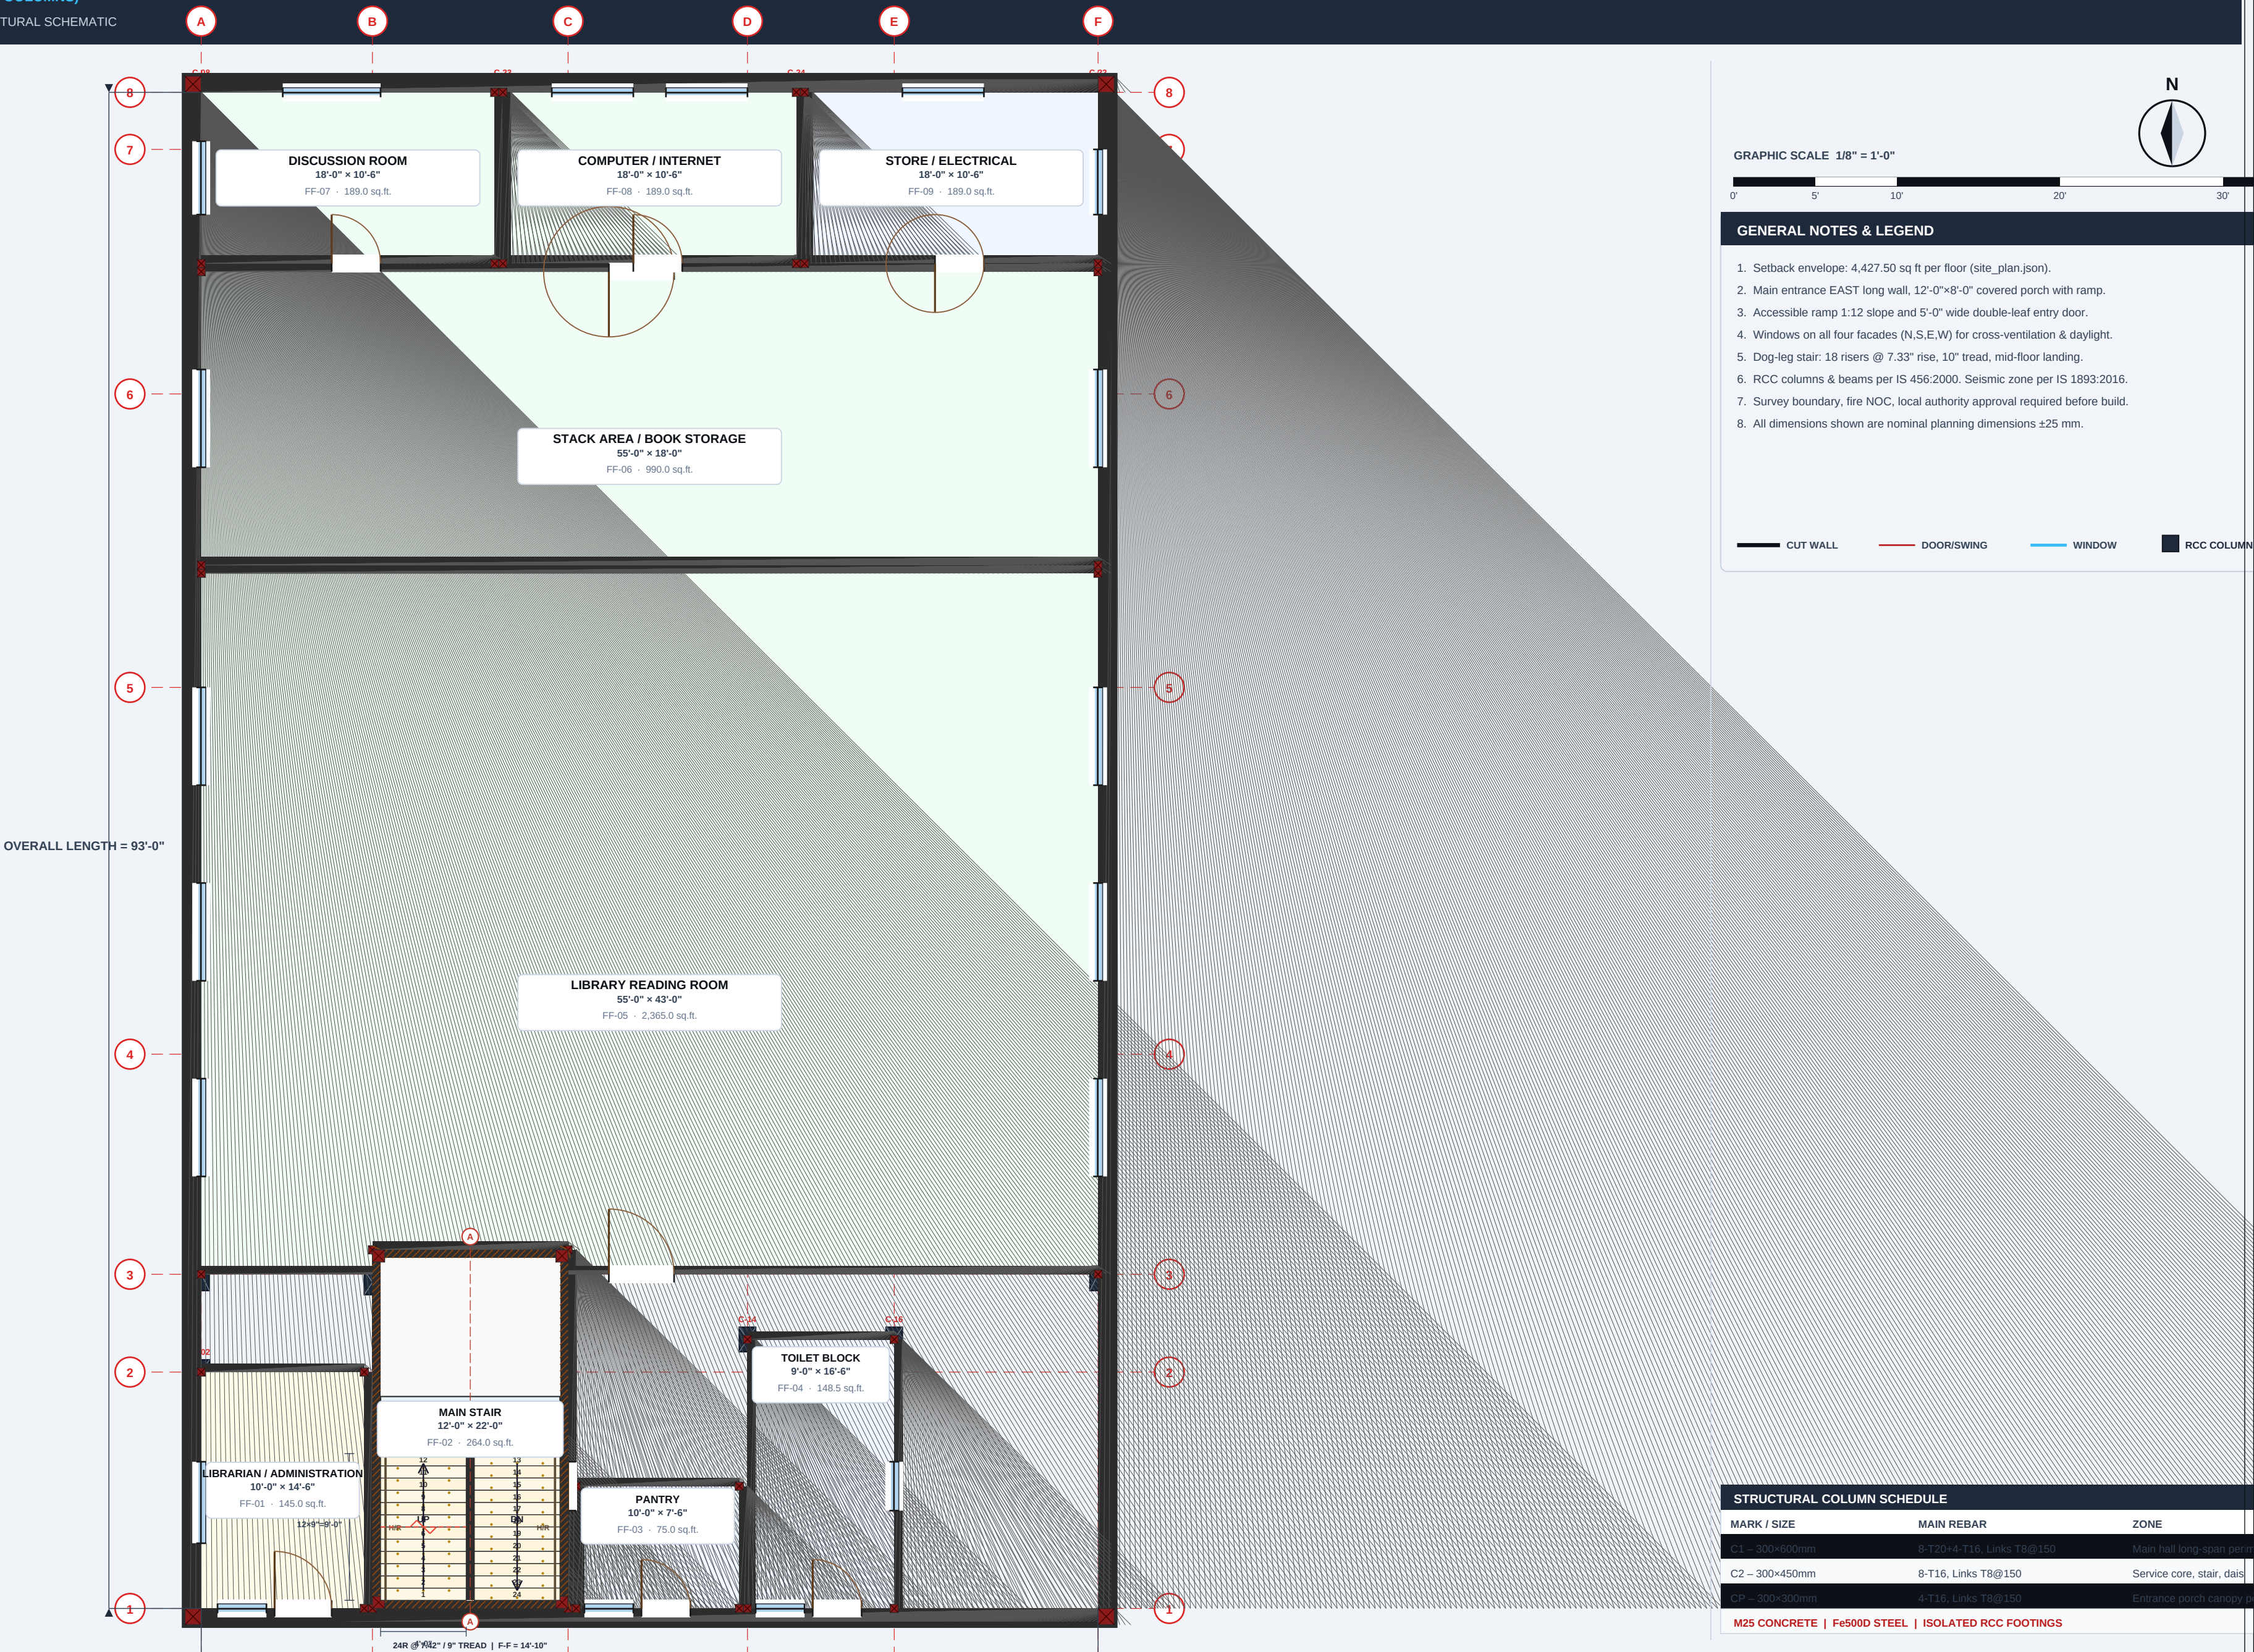

BAR ASSOCIATION HALL  
DISTRICT COURT COMPLEX, BANSWARA  
RAJASTHAN, INDIA

PLANNING SETBACK ENVELOPE: 4,427.50 SQ.FT. PER FLOOR  
MAIN ENTRY: EAST LONG WALL · WINDOWS: ALL FOUR SIDES

FIRST FLOOR PLAN  
STRUCTURAL COLUMN & GRID COORDINATION PLAN (WITH COLUMNS)  
LEVEL: FIRST FLOOR SCALE: 1/8" = 1'-0" (A2 LANDSCAPE)

STRUCTURE: RCC FRAME IS 456:2000 / IS 1893:2016  
STATUS: APPROVED SCHEMATIC — NOT FOR CONSTRUCTION

S-102

SHEET NO.

REV: P01  
18-SEP-2026