


A-101 | GROUND FLOOR PLAN

BAR ASSOCIATION HALL · BANSWARA · COORDINATED MODEL P01 · SCHEMATIC

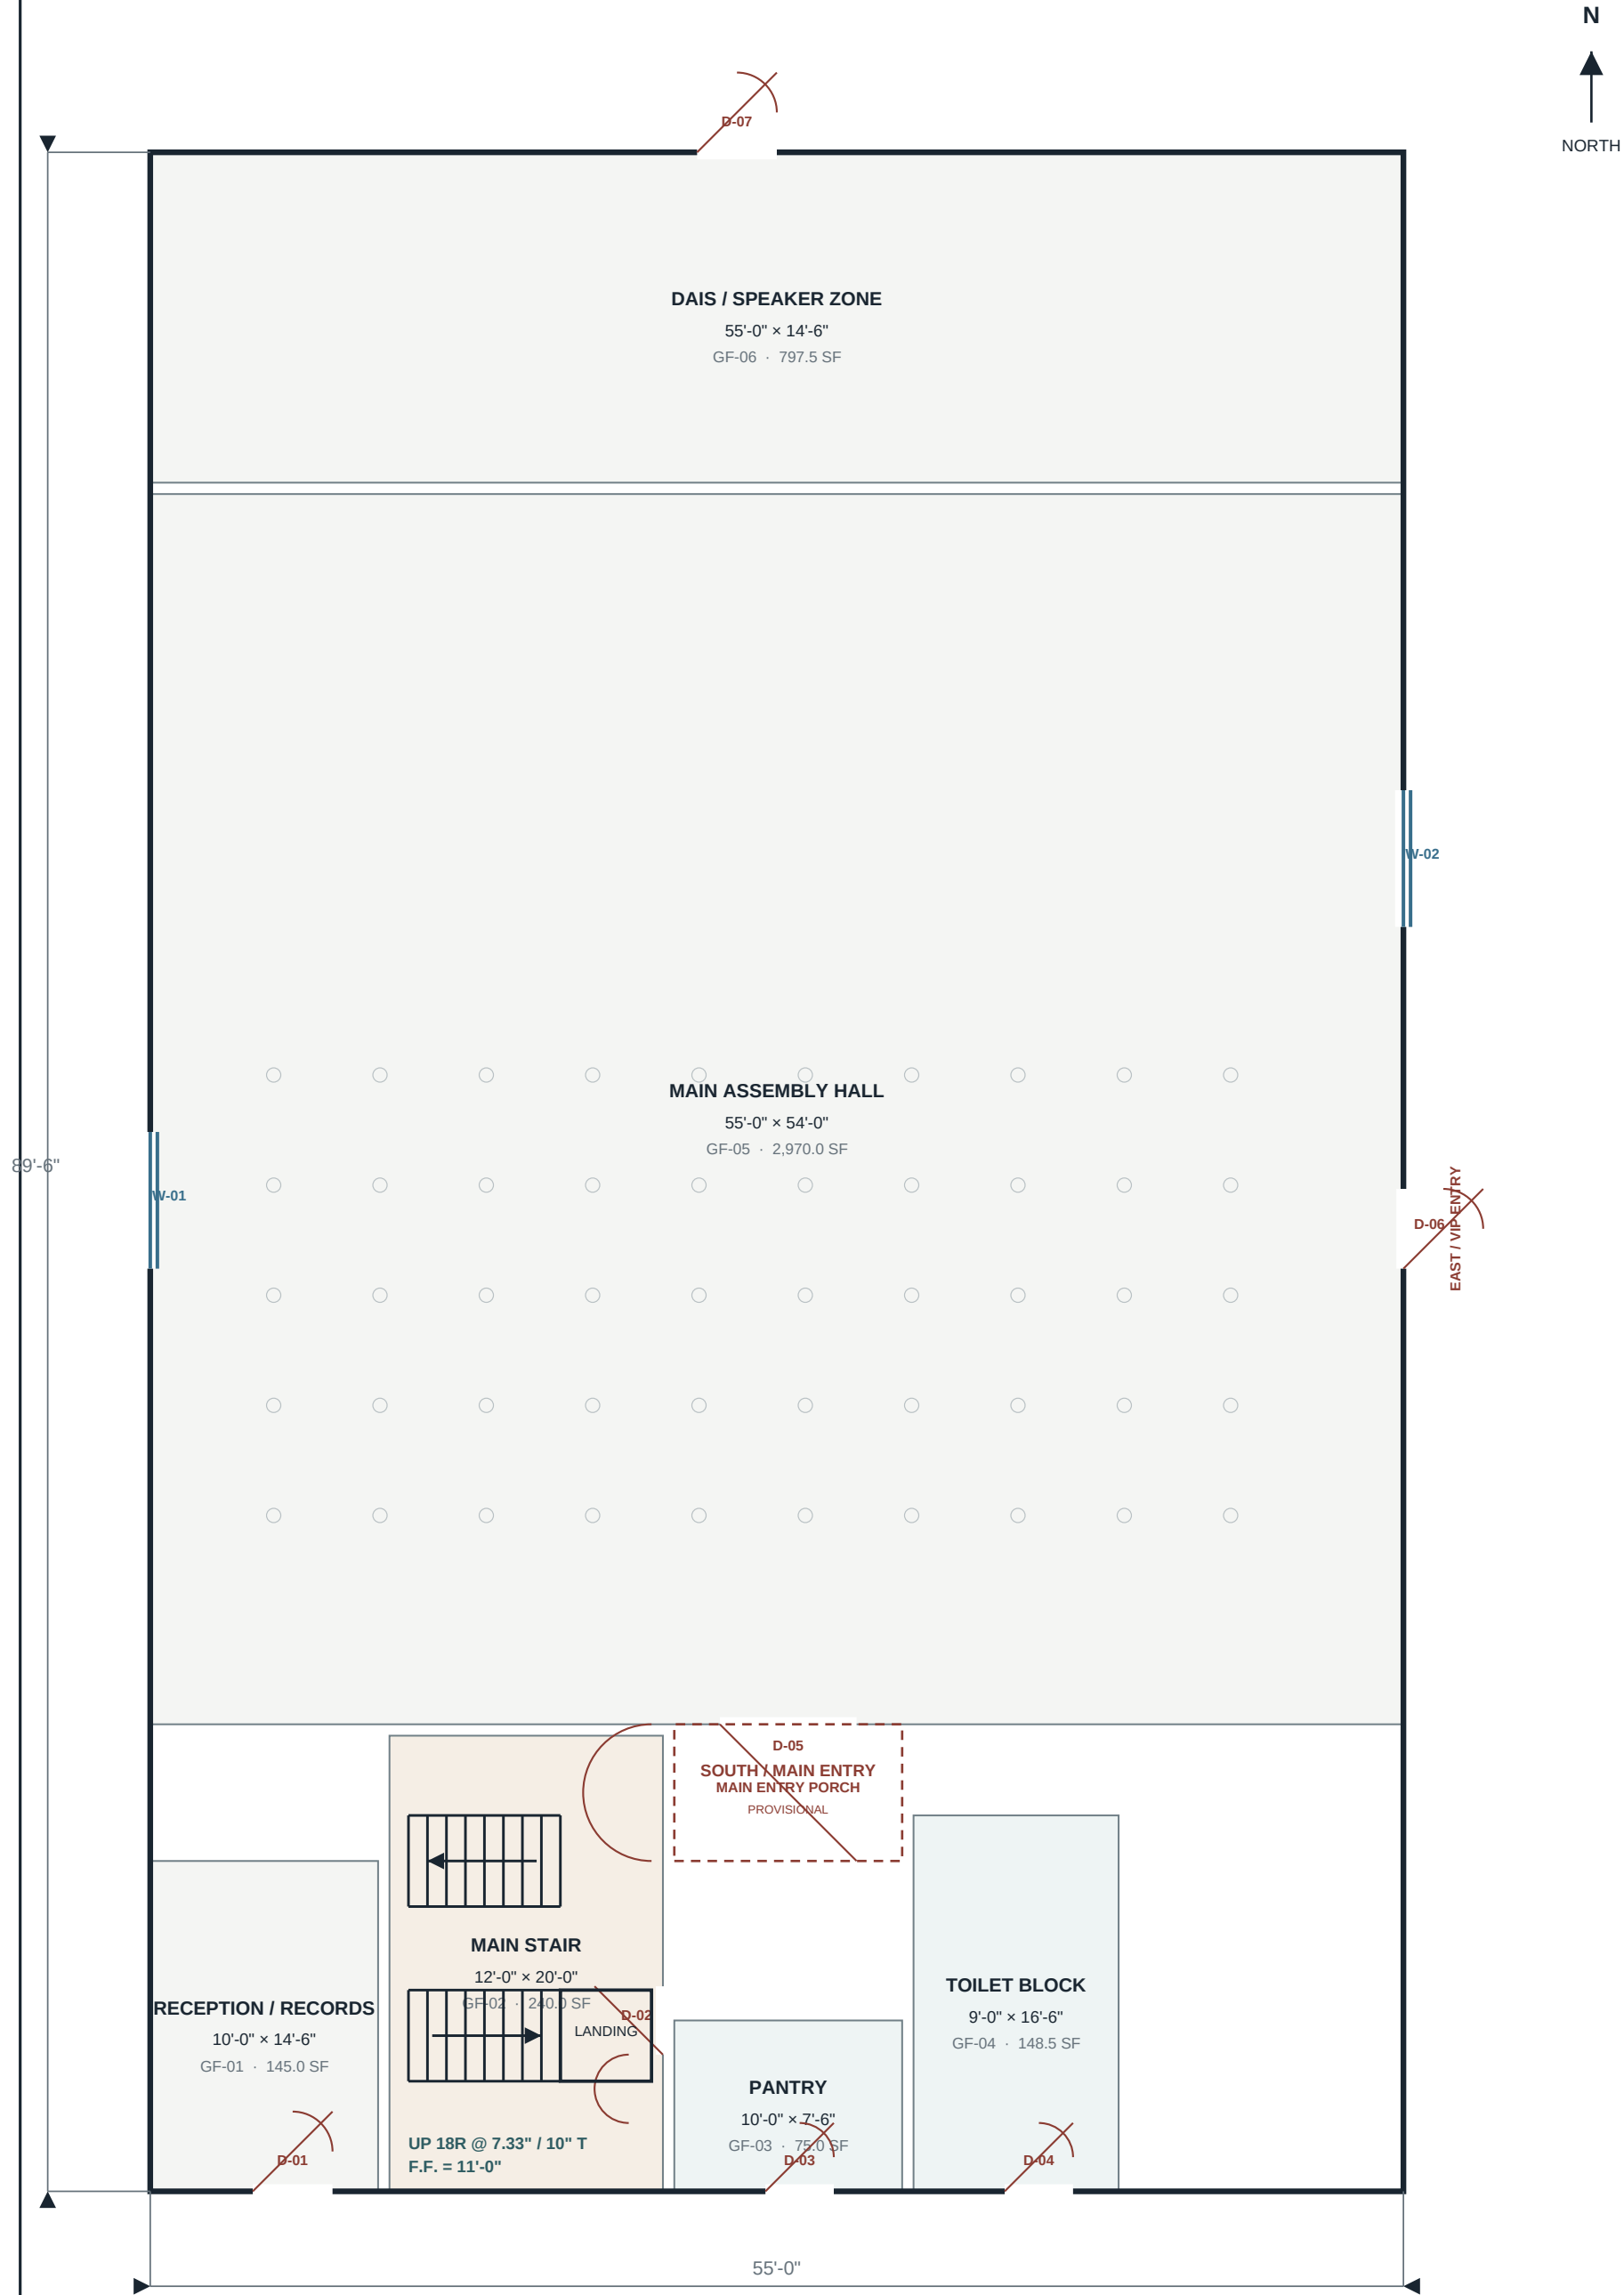

DRAWING NOTES

- Dimensions are in feet and inches unless noted otherwise.
- Cut walls are heavy; partitions and fixtures are lighter for legibility.
- D-tags identify door openings; W-tags identify window openings.
- Door symbols include a wall break, hinge, leaf, and 90° swing arc.
- Stair is a two-flight 180° dog-leg with a connecting landing.
- Confirm all dimensions against survey and issued consultant drawings.
- Local code, fire, accessibility, structure, MEP, and authority review remain required.

CUT WALL PARTITION / OPENING

SPACE SCHEDULE		
ID	SPACE	AREA SF
GF-01	Reception / Records	145.0
GF-02	Main Stair	240.0
GF-03	Pantry	75.0
GF-04	Toilet Block	148.5
GF-05	Main Assembly Hall	2,970.0
GF-06	Dais / Speaker Zone	797.5

BAR ASSOCIATION HALL

BANSWARA, RAJASTHAN

A-101

SHEET

PRELIMINARY / SCHEMATIC

GROUND FLOOR
NOT FOR CONSTRUCTION

REV P01