


A-101 | GROUND FLOOR PLAN

BAR ASSOCIATION HALL · BANSWARA · COORDINATED MODEL P01 · SCHEMATIC

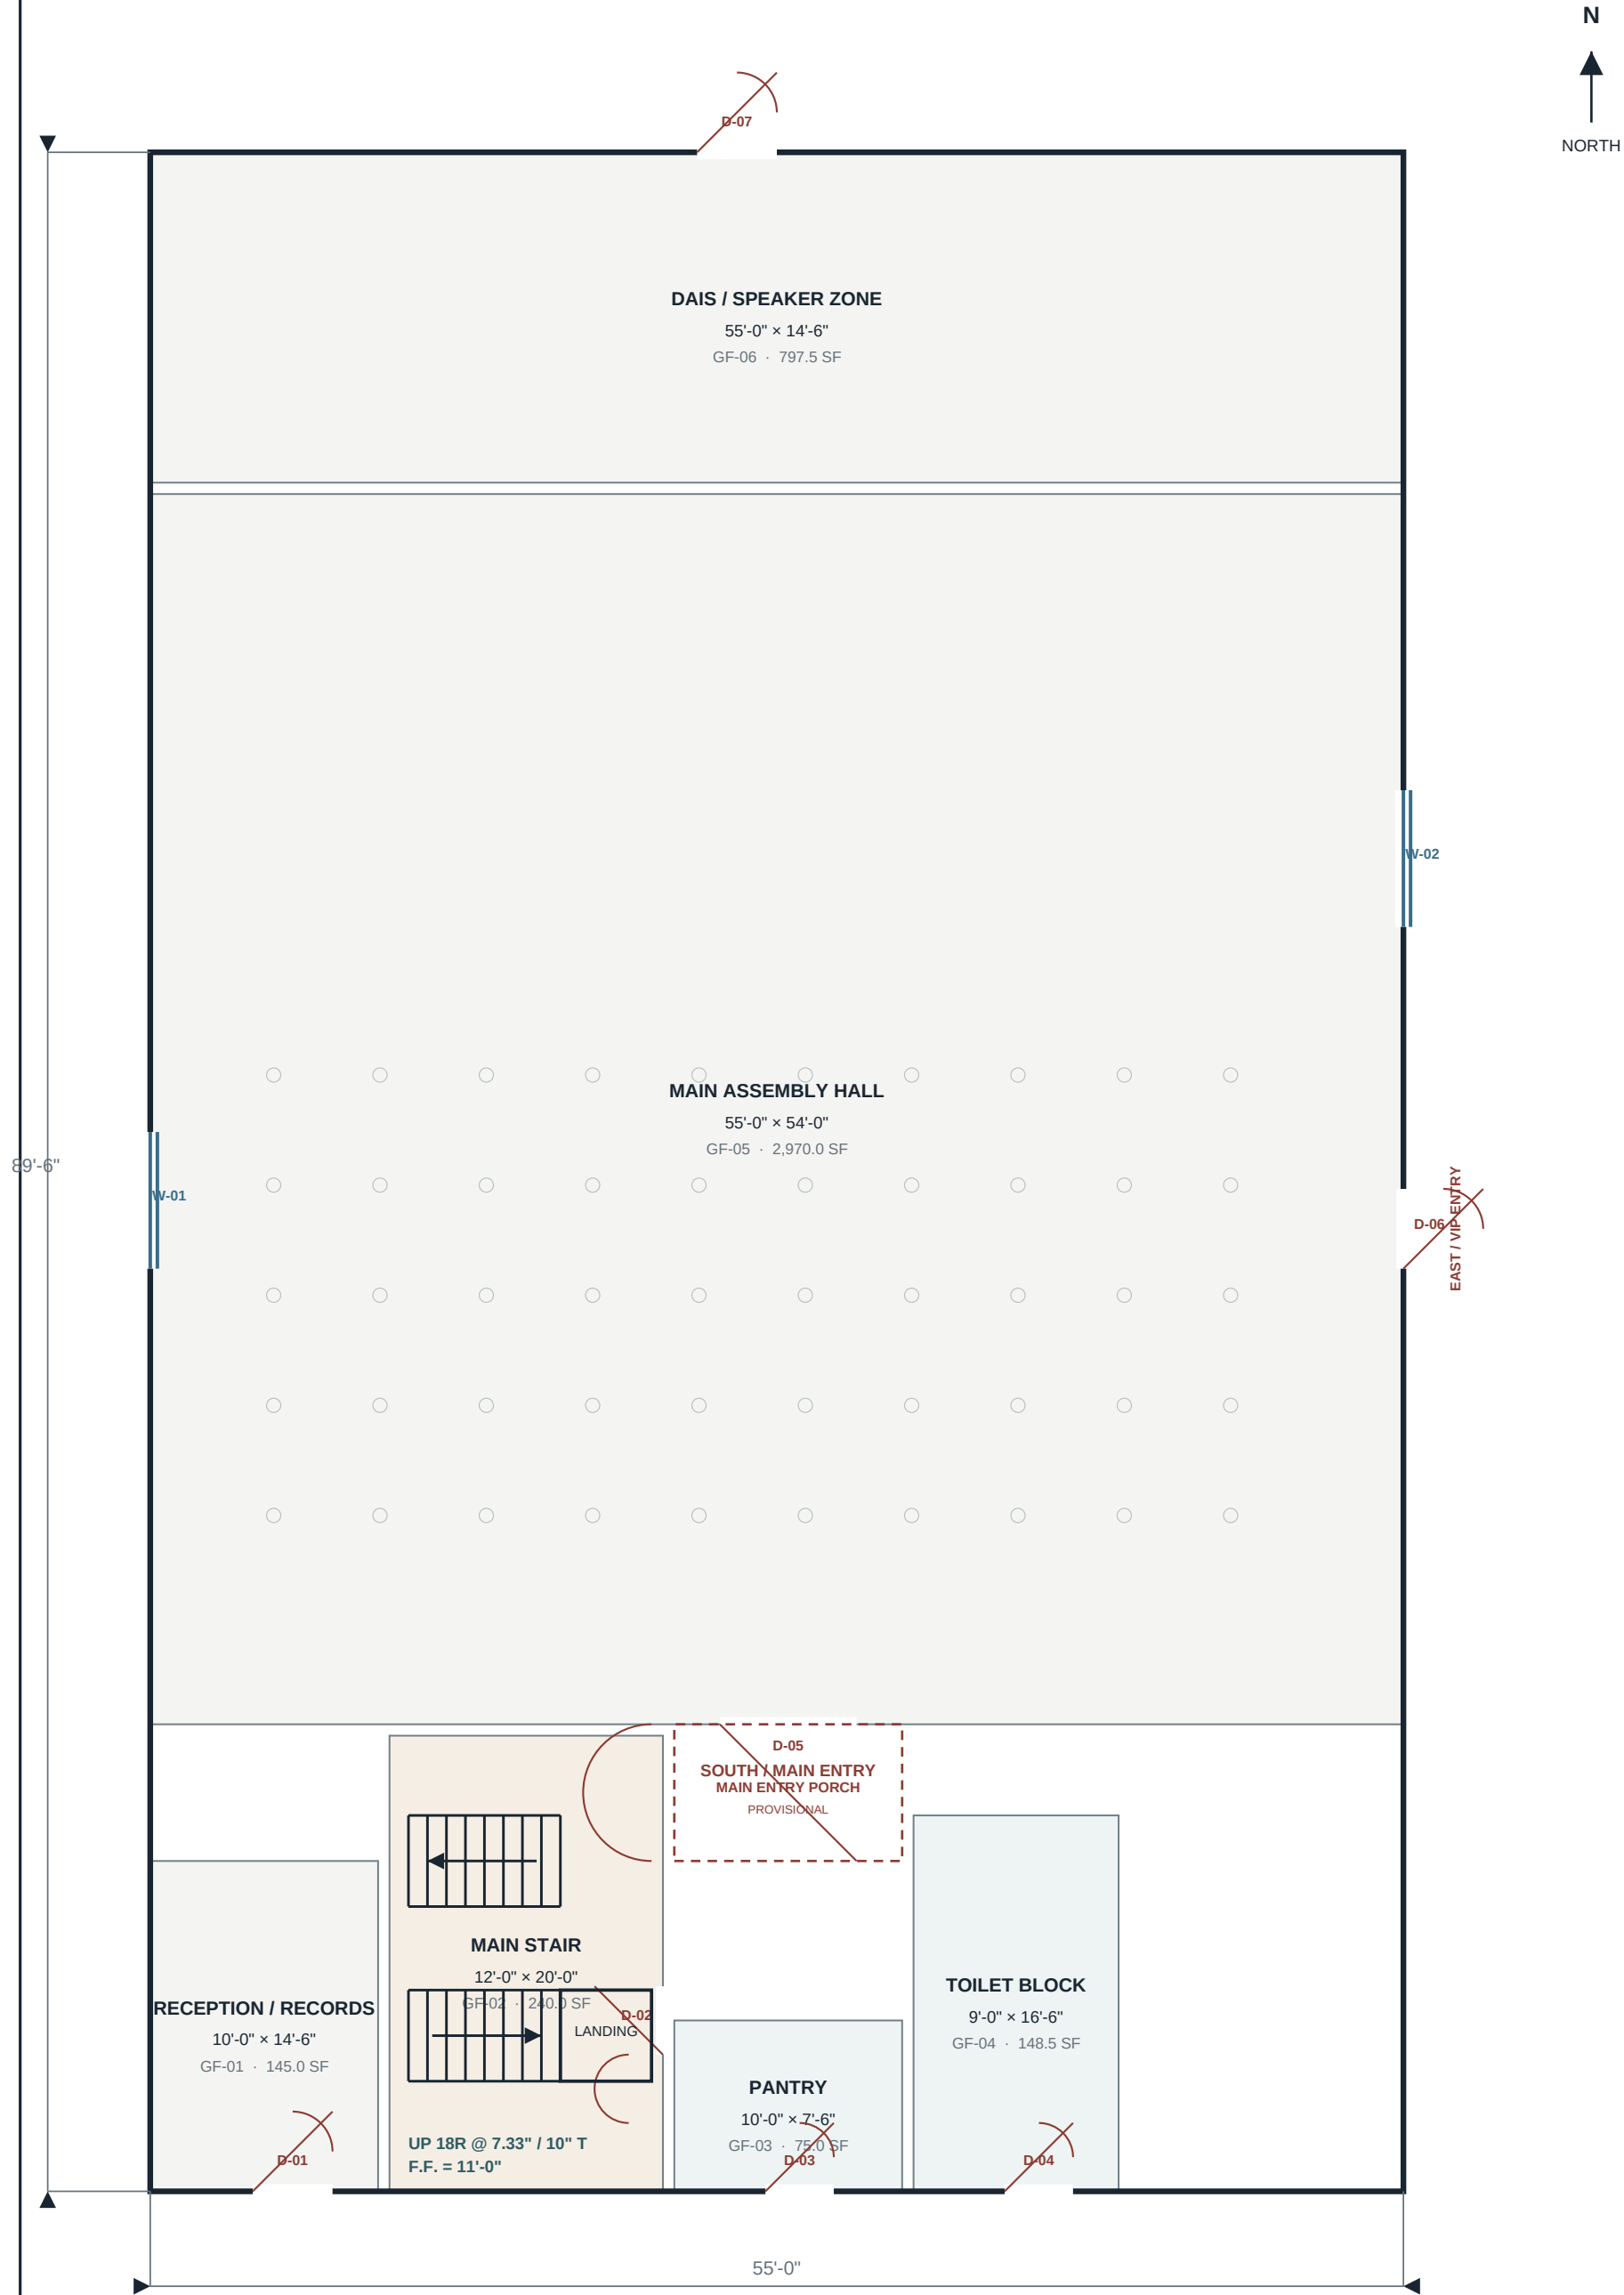

DRAWING NOTES

- Dimensions are in feet and inches unless noted otherwise.
- Cut walls are heavy; partitions and fixtures are lighter for legibility.
- D-tags identify door openings; W-tags identify window openings.
- Door symbols include a wall break, hinge, leaf, and 90° swing arc.
- Stair is a two-flight 180° dog-leg with a connecting landing.
- Confirm all dimensions against survey and issued consultant drawings.
- Local code, fire, accessibility, structure, MEP, and authority review remain required.

CUT WALL PARTITION / OPENING

SPACE SCHEDULE		
ID	SPACE	AREA SF
GF-01	Reception / Records	145.0
GF-02	Main Stair	240.0
GF-03	Pantry	75.0
GF-04	Toilet Block	148.5
GF-05	Main Assembly Hall	2,970.0
GF-06	Dais / Speaker Zone	797.5

BAR ASSOCIATION HALL

BANSWARA, RAJASTHAN

PRELIMINARY / SCHEMATIC

GROUND FLOOR
NOT FOR CONSTRUCTION

A-101

SHEET

REV P01

A-102 | FIRST FLOOR PLAN

BAR ASSOCIATION HALL · BANSWARA · COORDINATED MODEL P01 · SCHEMATIC



DRAWING NOTES

1. Dimensions are in feet and inches unless noted otherwise.
2. Cut walls are heavy; partitions and fixtures are lighter for legibility.
3. D-tags identify door openings; W-tags identify window openings.
4. Door symbols include a wall break, hinge, leaf, and 90° swing arc.
5. Stair is a two-flight 180° dog-leg with a connecting landing.
6. Confirm all dimensions against survey and issued consultant drawings.
7. Local code, fire, accessibility, structure, MEP, and authority review remain required.

CUT WALL PARTITION / OPENING

SPACE SCHEDULE		
ID	SPACE	AREA SF
FF-01	Librarian / Administration	145.0
FF-02	Main Stair	240.0
FF-03	Pantry	75.0
FF-04	Toilet Block	148.5
FF-05	Library Reading Room	2,365.0
FF-06	Stack Area / Book Storage	990.0
FF-07	Discussion Room	189.0
FF-08	Computer / Internet	189.0
FF-09	Store / Electrical	189.0

BAR ASSOCIATION HALL

BANSWARA, RAJASTHAN

PRELIMINARY / SCHEMATIC

FIRST FLOOR
NOT FOR CONSTRUCTION

A-102

SHEET

REV P01