


SP-101 | GROUND FLOOR — SEATING ARRANGEMENT PLAN

AUDIENCE : 560 PVC CHAIRS | DAIS : 12 EXECUTIVE CHAIRS | TOTAL : 572 SEATS

BANSWARA DISTRICT COURT COMPLEX, RAJASTHAN · SEATING LAYOUT — FOR REVIEW

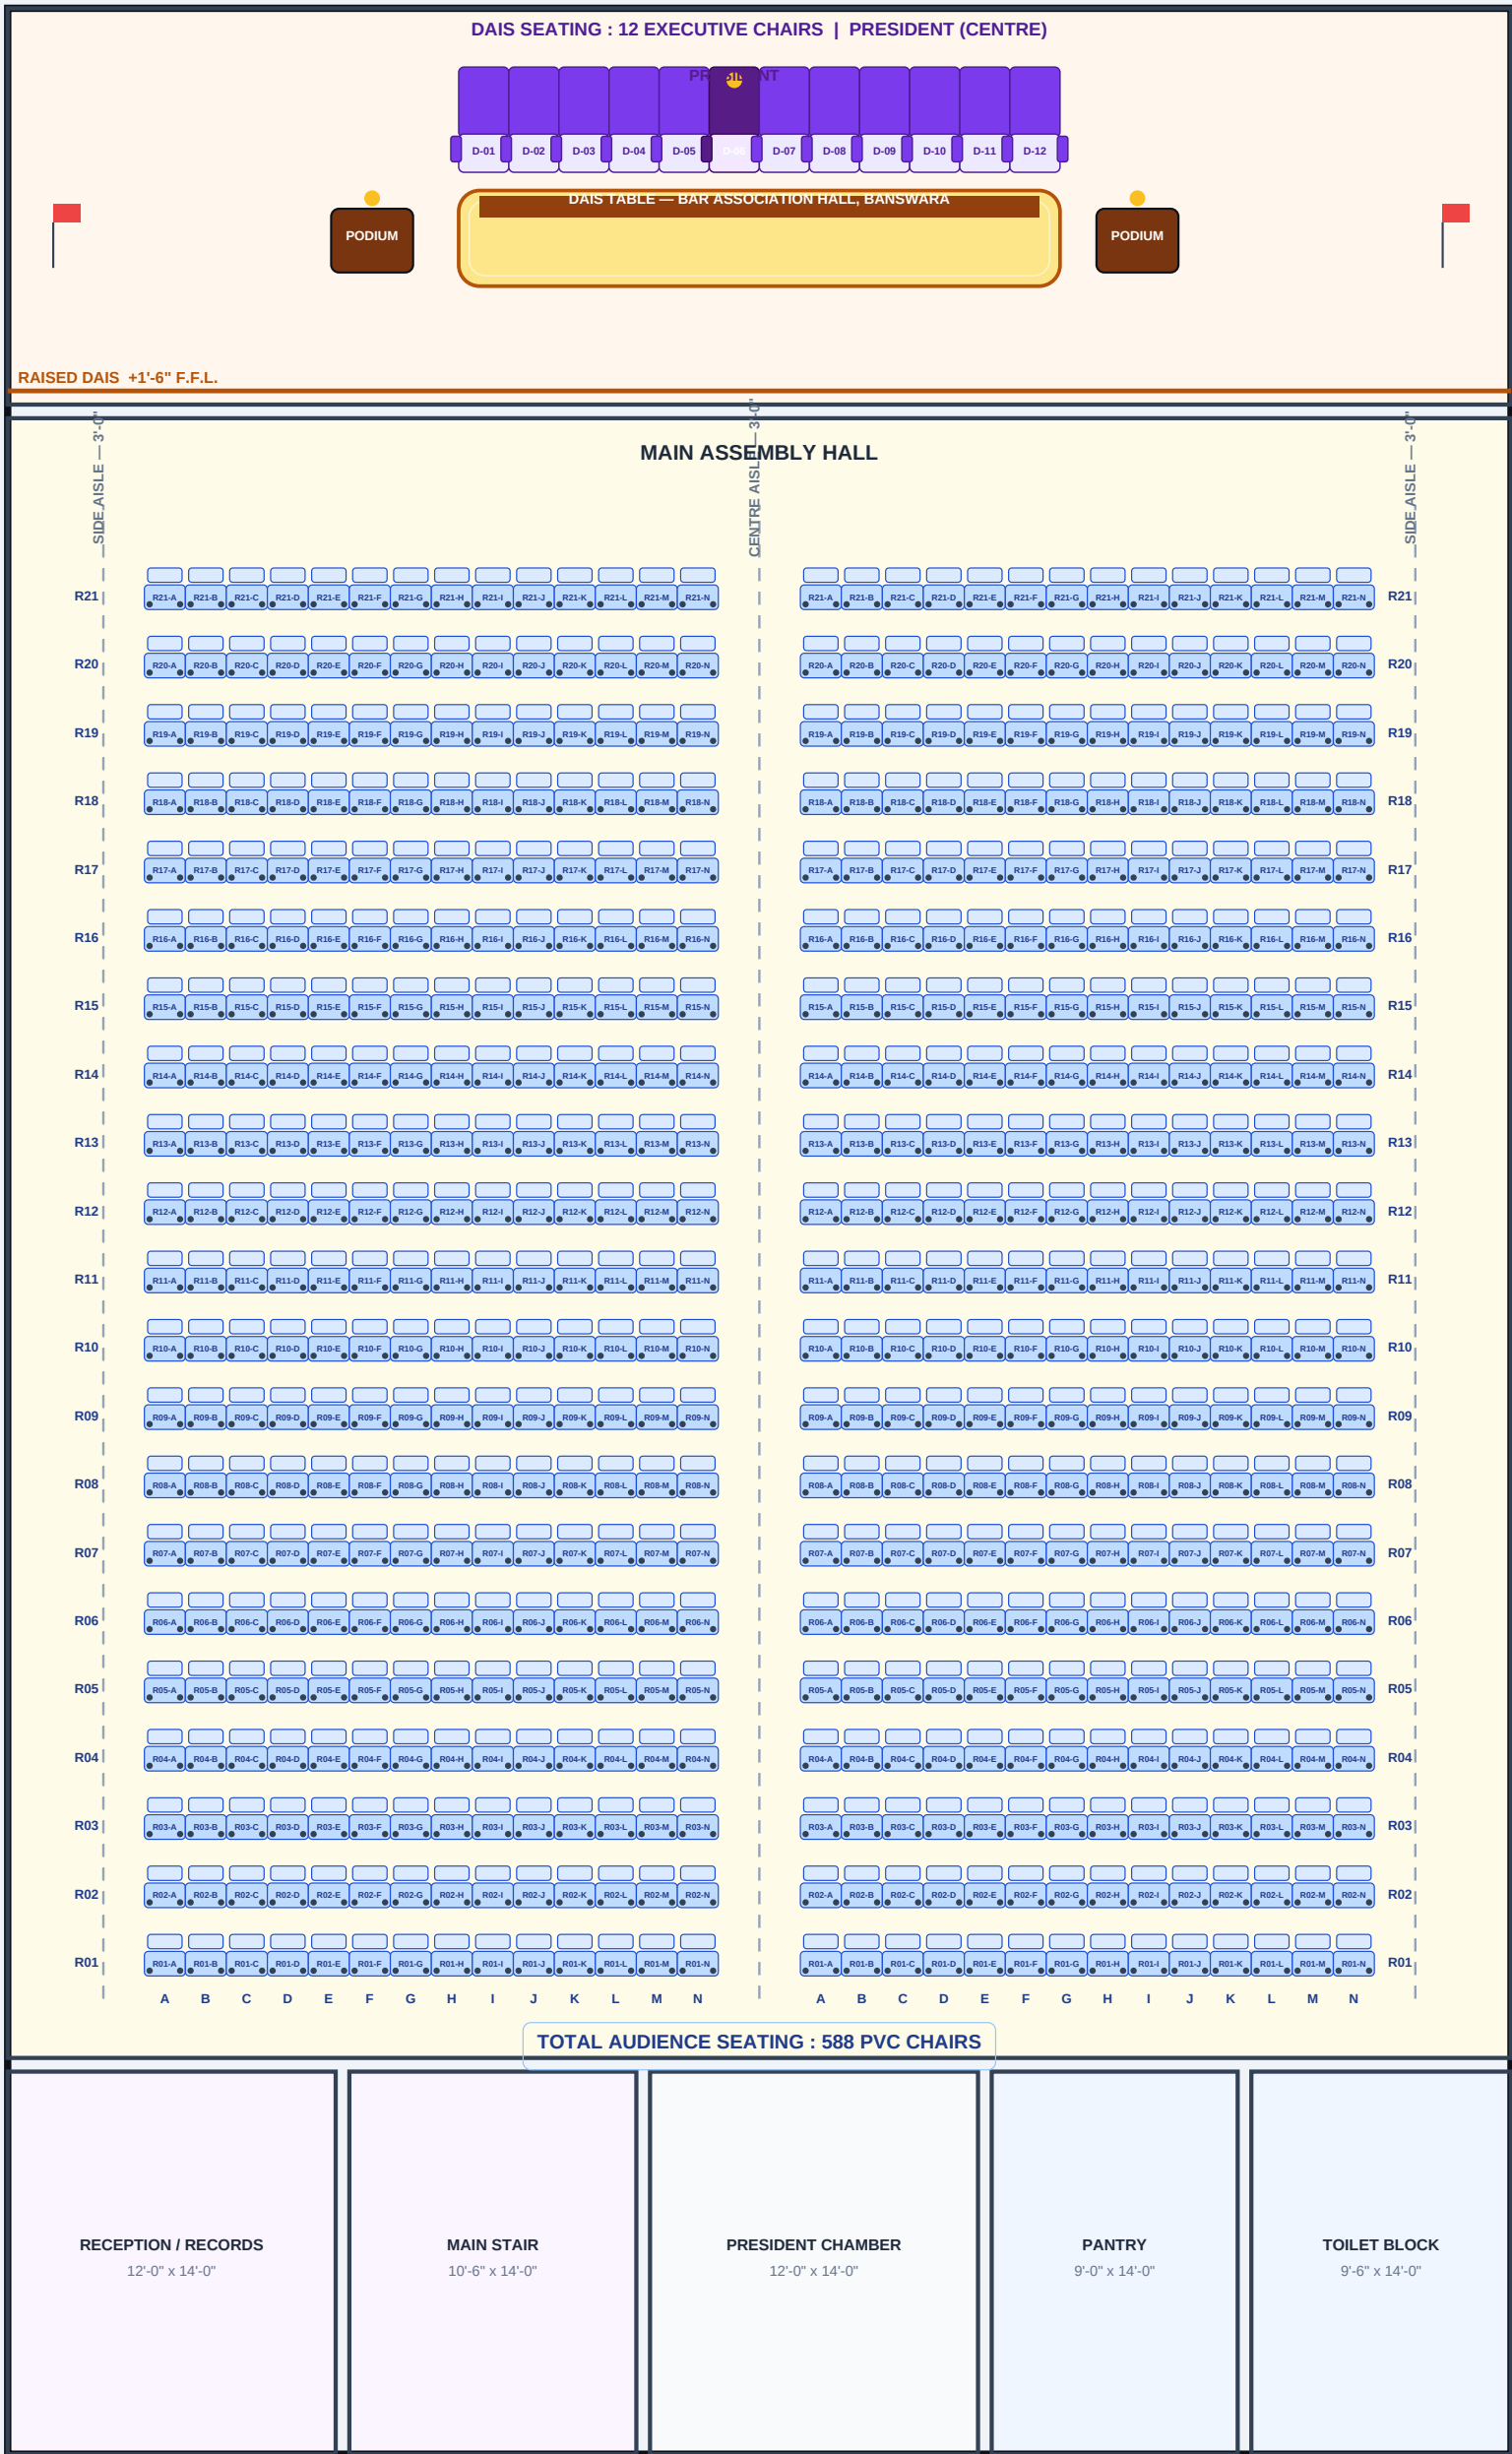

SEATING LEGEND & NOTES

- PVC AUDIENCE CHAIR (18"×18")
- EXECUTIVE CHAIR — DAIS (HIGH-BACK)
- DAIS TABLE (CURVED, HIGH-GLOSS FINISH)
- ACCESS AISLE (3'-0" CLEAR MIN.)

- Audience PVC chairs: 2 side aisles 3'-0" + 1 centre aisle 3'-0".
- Row pitch: 30" (back of seat to back of next seat).
- Rows numbered R01–R20 front (dais) to rear. Cols A–N each block.
- Each seat marked: R01-A ... R20-N (left & right blocks identical).
- Dais seats: D-01 (leftmost) to D-12 (rightmost). D-06 = President.
- Wheelchair spaces: 4 positions at front sides (not shown).

SEATING CAPACITY SUMMARY

ZONE	SIZE	AREA	SEATING
Assembly Hall	55'-0" × 57'-0"	3,135 sq ft	Audience PVC Chairs
Dais / Speaker Zone	55'-0" × 14'-6"	797.5 sq ft	12 Executive Chairs
Total Seating Area	G.F. Only	3,932.5 sq ft	572 Seats Total

BAR ASSOCIATION HALL
DISTRICT COURT COMPLEX, BANSWARA
RAJASTHAN, INDIA

AUDIENCE: 560 PVC CHAIRS | DAIS: 12 EXEC. CHAIRS
MAIN ENTRY: EAST LONG WALL · 4-SIDED FENESTRATION

GROUND FLOOR — SEATING ARRANGEMENT PLAN
SEATING LAYOUT PLAN

LEVEL: GROUND FLOOR SCALE: 1/8" = 1'-0" (A2 LANDSCAPE)

PVC CHAIR: 18"×18" SEAT | ROW PITCH: 30" | 3 AISLES
STATUS: FOR REVIEW — NOT FOR CONSTRUCTION

SP-101

SHEET NO.

REV: P01
18-SEP-2026