


A-102 | FIRST FLOOR PLAN

ARCHITECTURAL FLOOR PLAN (WITHOUT FURNITURE)

BANSWARA DISTRICT COURT COMPLEX · COORDINATED ARCHITECTURAL SCHEMATIC

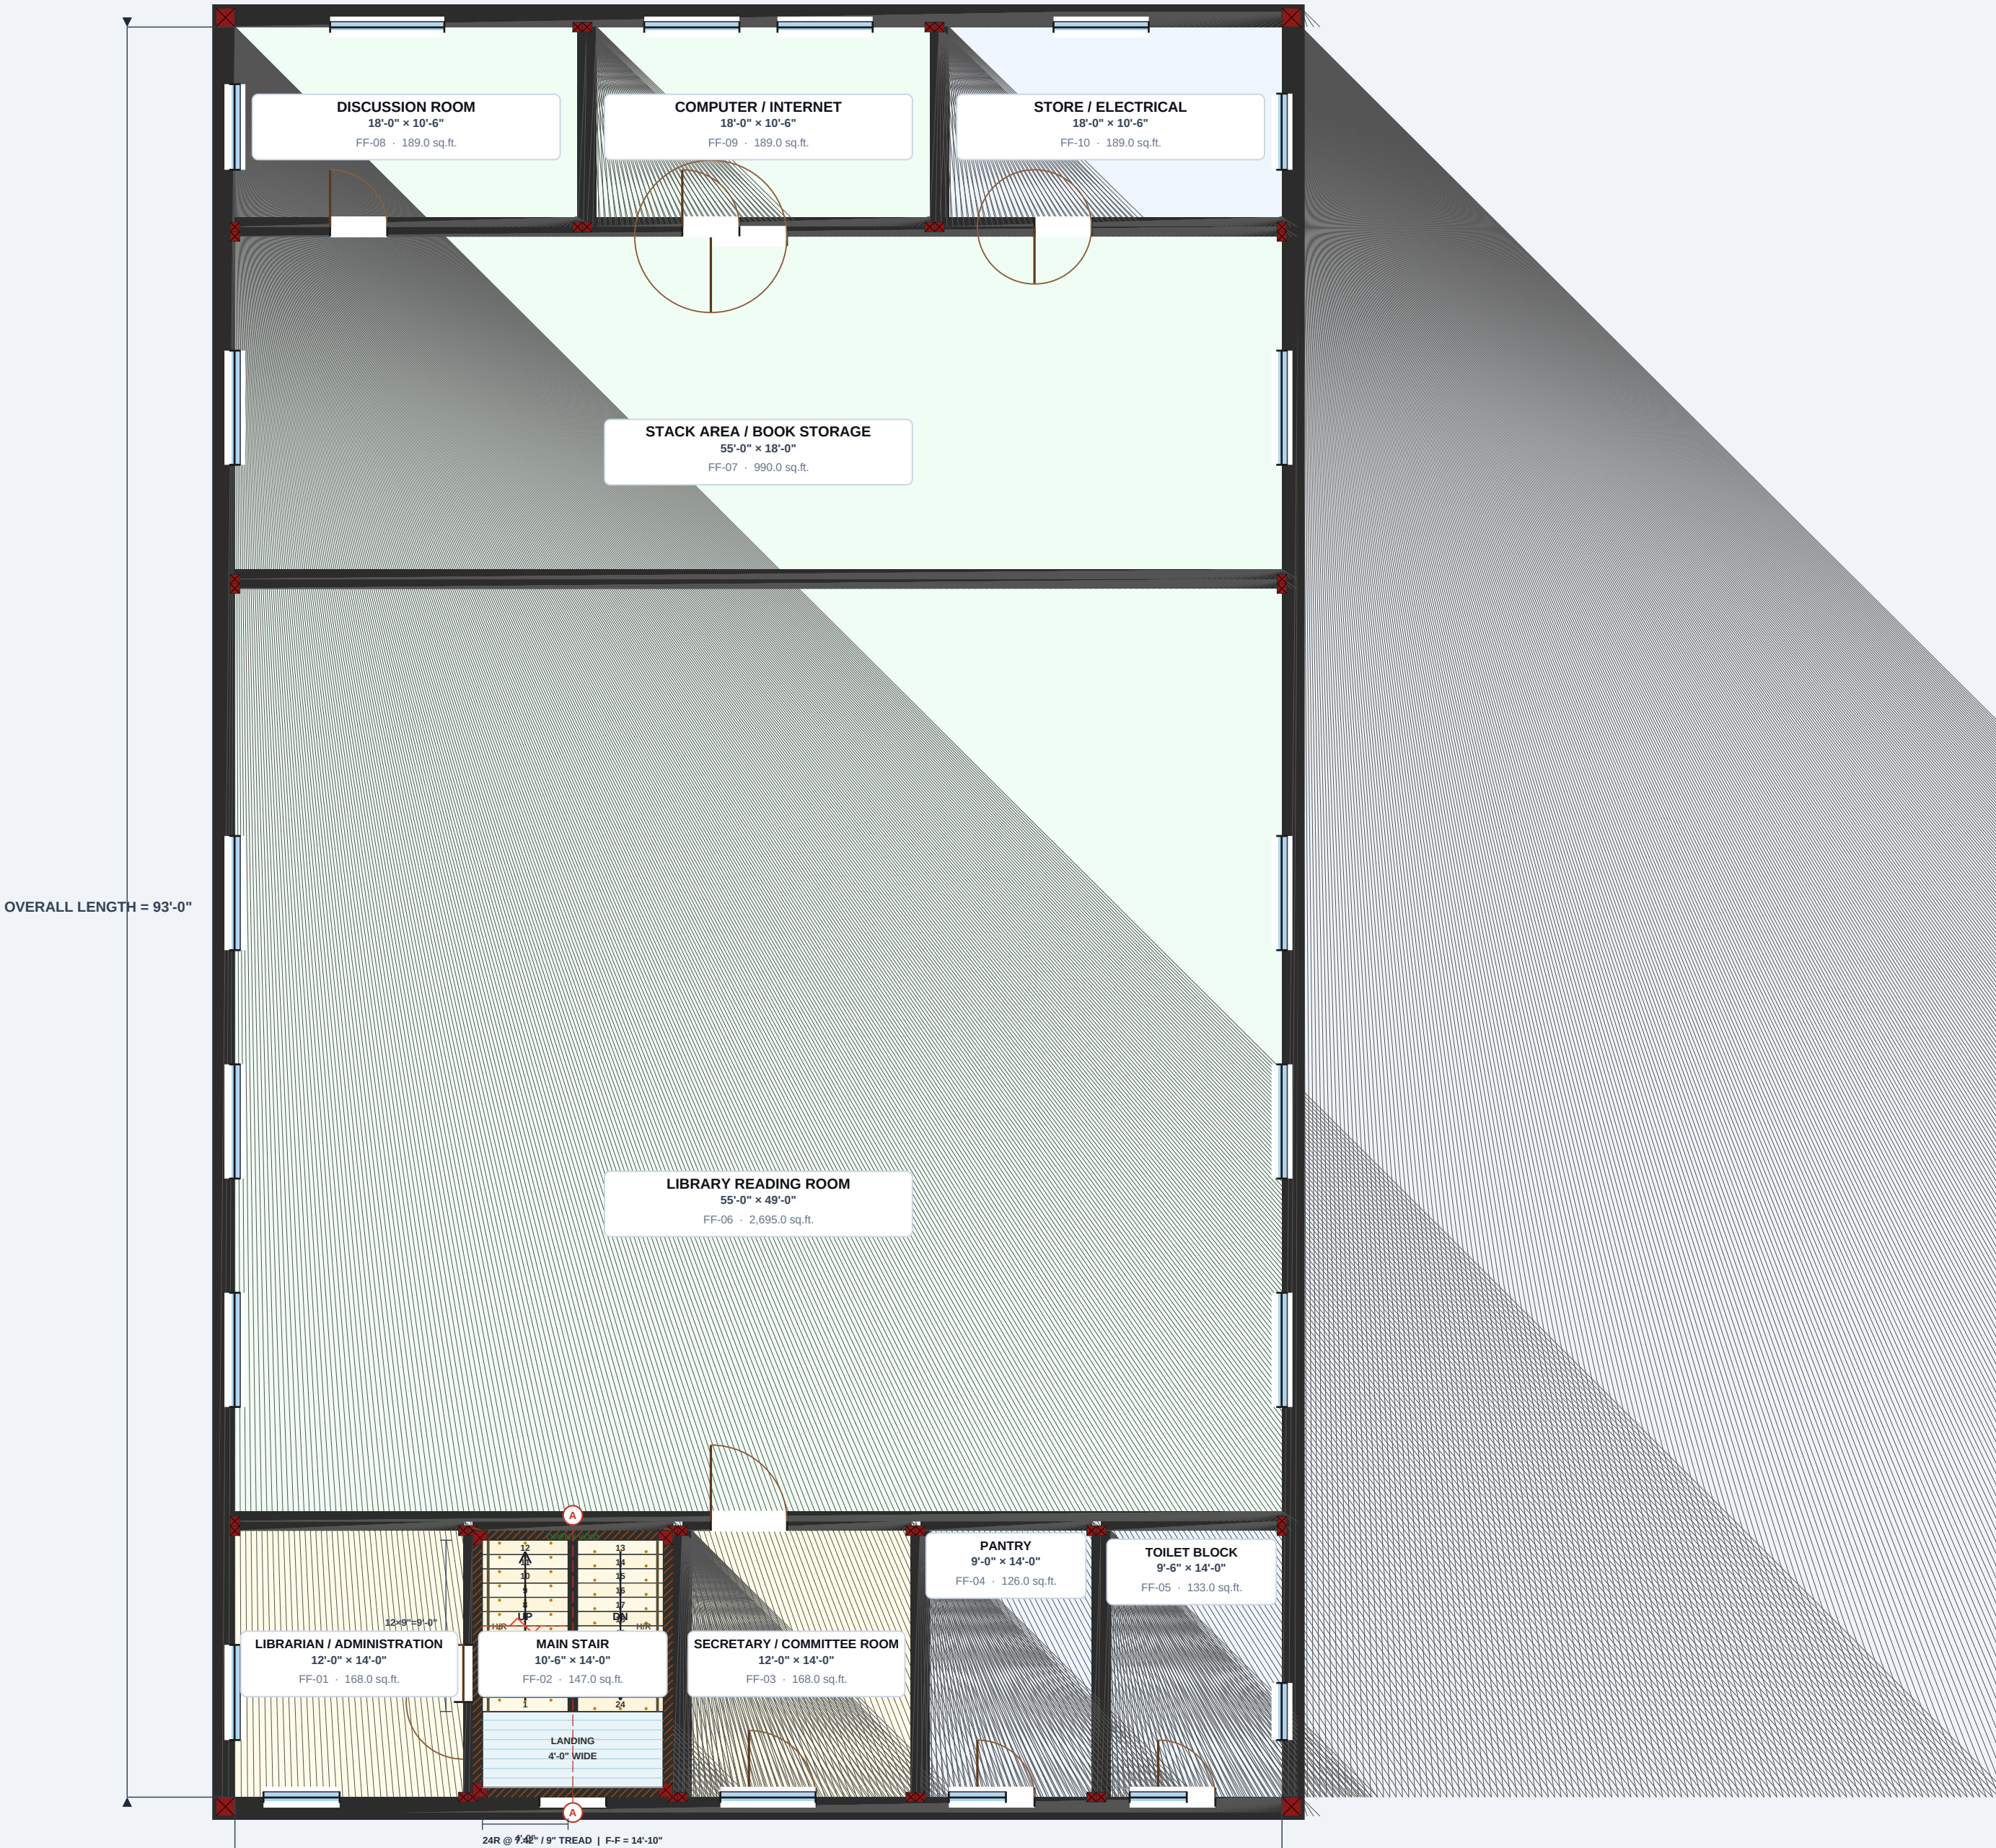

GRAPHIC SCALE 1/8" = 1'-0"

0' 5' 10' 20' 30'

GENERAL NOTES & LEGEND

- Setback envelope: 4,427.50 sq ft per floor (site_plan.json).
- Main entrance EAST long wall, 12'-0"×8'-0" covered porch with ramp.
- Accessible ramp 1:12 slope and 5'-0" wide double-leaf entry door.
- Windows on all four facades (N,S,E,W) for cross-ventilation & daylight.
- Dog-leg stair: 18 risers @ 7.33" rise, 10" tread, mid-floor landing.
- RCC columns & beams per IS 456:2000. Seismic zone per IS 1893:2016.
- Survey boundary, fire NOC, local authority approval required before build.
- All dimensions shown are nominal planning dimensions ±25 mm.

CUT WALL DOOR/SWING WINDOW

ROOM / SPACE SCHEDULE

ID	SPACE NAME	SIZE
FF-01	Librarian / Administration	12'-0" × 14'-0"
FF-02	Main Stair	10'-6" × 14'-0"
FF-03	Secretary / Committee Room	12'-0" × 14'-0"
FF-04	Pantry	9'-0" × 14'-0"
FF-05	Toilet Block	9'-6" × 14'-0"
FF-06	Library Reading Room	55'-0" × 49'-0"
FF-07	Stack Area / Book Storage	55'-0" × 18'-0"
FF-08	Discussion Room	18'-0" × 10'-6"
FF-09	Computer / Internet	18'-0" × 10'-6"
TOTAL ADOPTABLE AREA		

BAR ASSOCIATION HALL
DISTRICT COURT COMPLEX, BANSWARA
RAJASTHAN, INDIA

PLANNING SETBACK ENVELOPE: 4,427.50 SQ.FT. PER FLOOR
MAIN ENTRY: EAST LONG WALL · WINDOWS: ALL FOUR SIDES

FIRST FLOOR PLAN
ARCHITECTURAL FLOOR PLAN (WITHOUT FURNITURE)
LEVEL: FIRST FLOOR SCALE: 1/8" = 1'-0" (A2 LANDSCAPE)

STRUCTURE: RCC FRAME IS 456:2000 / IS 1893:2016
STATUS: APPROVED SCHEMATIC — NOT FOR CONSTRUCTION

A-102

SHEET NO.

REV: P01
18-SEP-2026