

BAR ASSOCIATION HALL

DISTRICT COURT COMPLEX, BANSWARA, RAJASTHAN

COMPREHENSIVE ARCHITECTURAL & STRUCTURAL REVIEW SET · G+1 BUILDING

PROJECT	Bar Association Hall, Banswara
LOCATION	District Court Complex, Banswara, Rajasthan, India
BUILDING TYPE	Bar Association Hall — G+1 (Ground + First Floor)
PLANNING AREA	4,427.50 sq.ft. per floor (Setback Envelope)
MAIN ENTRANCE	East Long Wall — 12'-0" × 8'-0" Covered Porch
FENESTRATION	All Four Facades (North, South, East, West)
STRUCTURE	RCC Framed — IS 456:2000 / IS 1893:2016
SCALE	1/8" = 1'-0" Sheet: A2 Landscape
DATE	18-SEP-2026
REVISION	P01 — Approved Schematic
STATUS	APPROVED SCHEMATIC DESIGN — NOT FOR CONSTRUCTION

SHEET INDEX

A-101	A-201	S-101	A-102	A-202	S-102
GROUND FLOOR PLAN GF BARE / NO FURN.	GROUND FLOOR PLAN GF WITH FURNITURE	GROUND FLOOR PLAN GF WITH COLUMNS	FIRST FLOOR PLAN FF BARE / NO FURN.	FIRST FLOOR PLAN FF WITH FURNITURE	FIRST FLOOR PLAN FF WITH COLUMNS

A-101 | GROUND FLOOR PLAN

ARCHITECTURAL FLOOR PLAN (WITHOUT FURNITURE)

BANSWARA DISTRICT COURT COMPLEX · COORDINATED ARCHITECTURAL SCHEMATIC



BAR ASSOCIATION HALL
DISTRICT COURT COMPLEX, BANSWARA
RAJASTHAN, INDIA

PLANNING SETBACK ENVELOPE: 4,427.50 SQ.FT. PER FLOOR
MAIN ENTRY: EAST LONG WALL · WINDOWS: ALL FOUR SIDES

GROUND FLOOR PLAN
ARCHITECTURAL FLOOR PLAN (WITHOUT FURNITURE)
LEVEL: GROUND FLOOR SCALE: 1/8" = 1'-0" (A2 LANDSCAPE)

STRUCTURE: RCC FRAME IS 456:2000 / IS 1893:2016
STATUS: APPROVED SCHEMATIC — NOT FOR CONSTRUCTION

A-101

SHEET NO.


REV: P01
18-SEP-2026

A-201 | GROUND FLOOR PLAN

PRESENTATION FLOOR PLAN (WITH FURNITURE)

BANSWARA DISTRICT COURT COMPLEX · COORDINATED ARCHITECTURAL SCHEMATIC

OVERALL LENGTH = 89'-6"

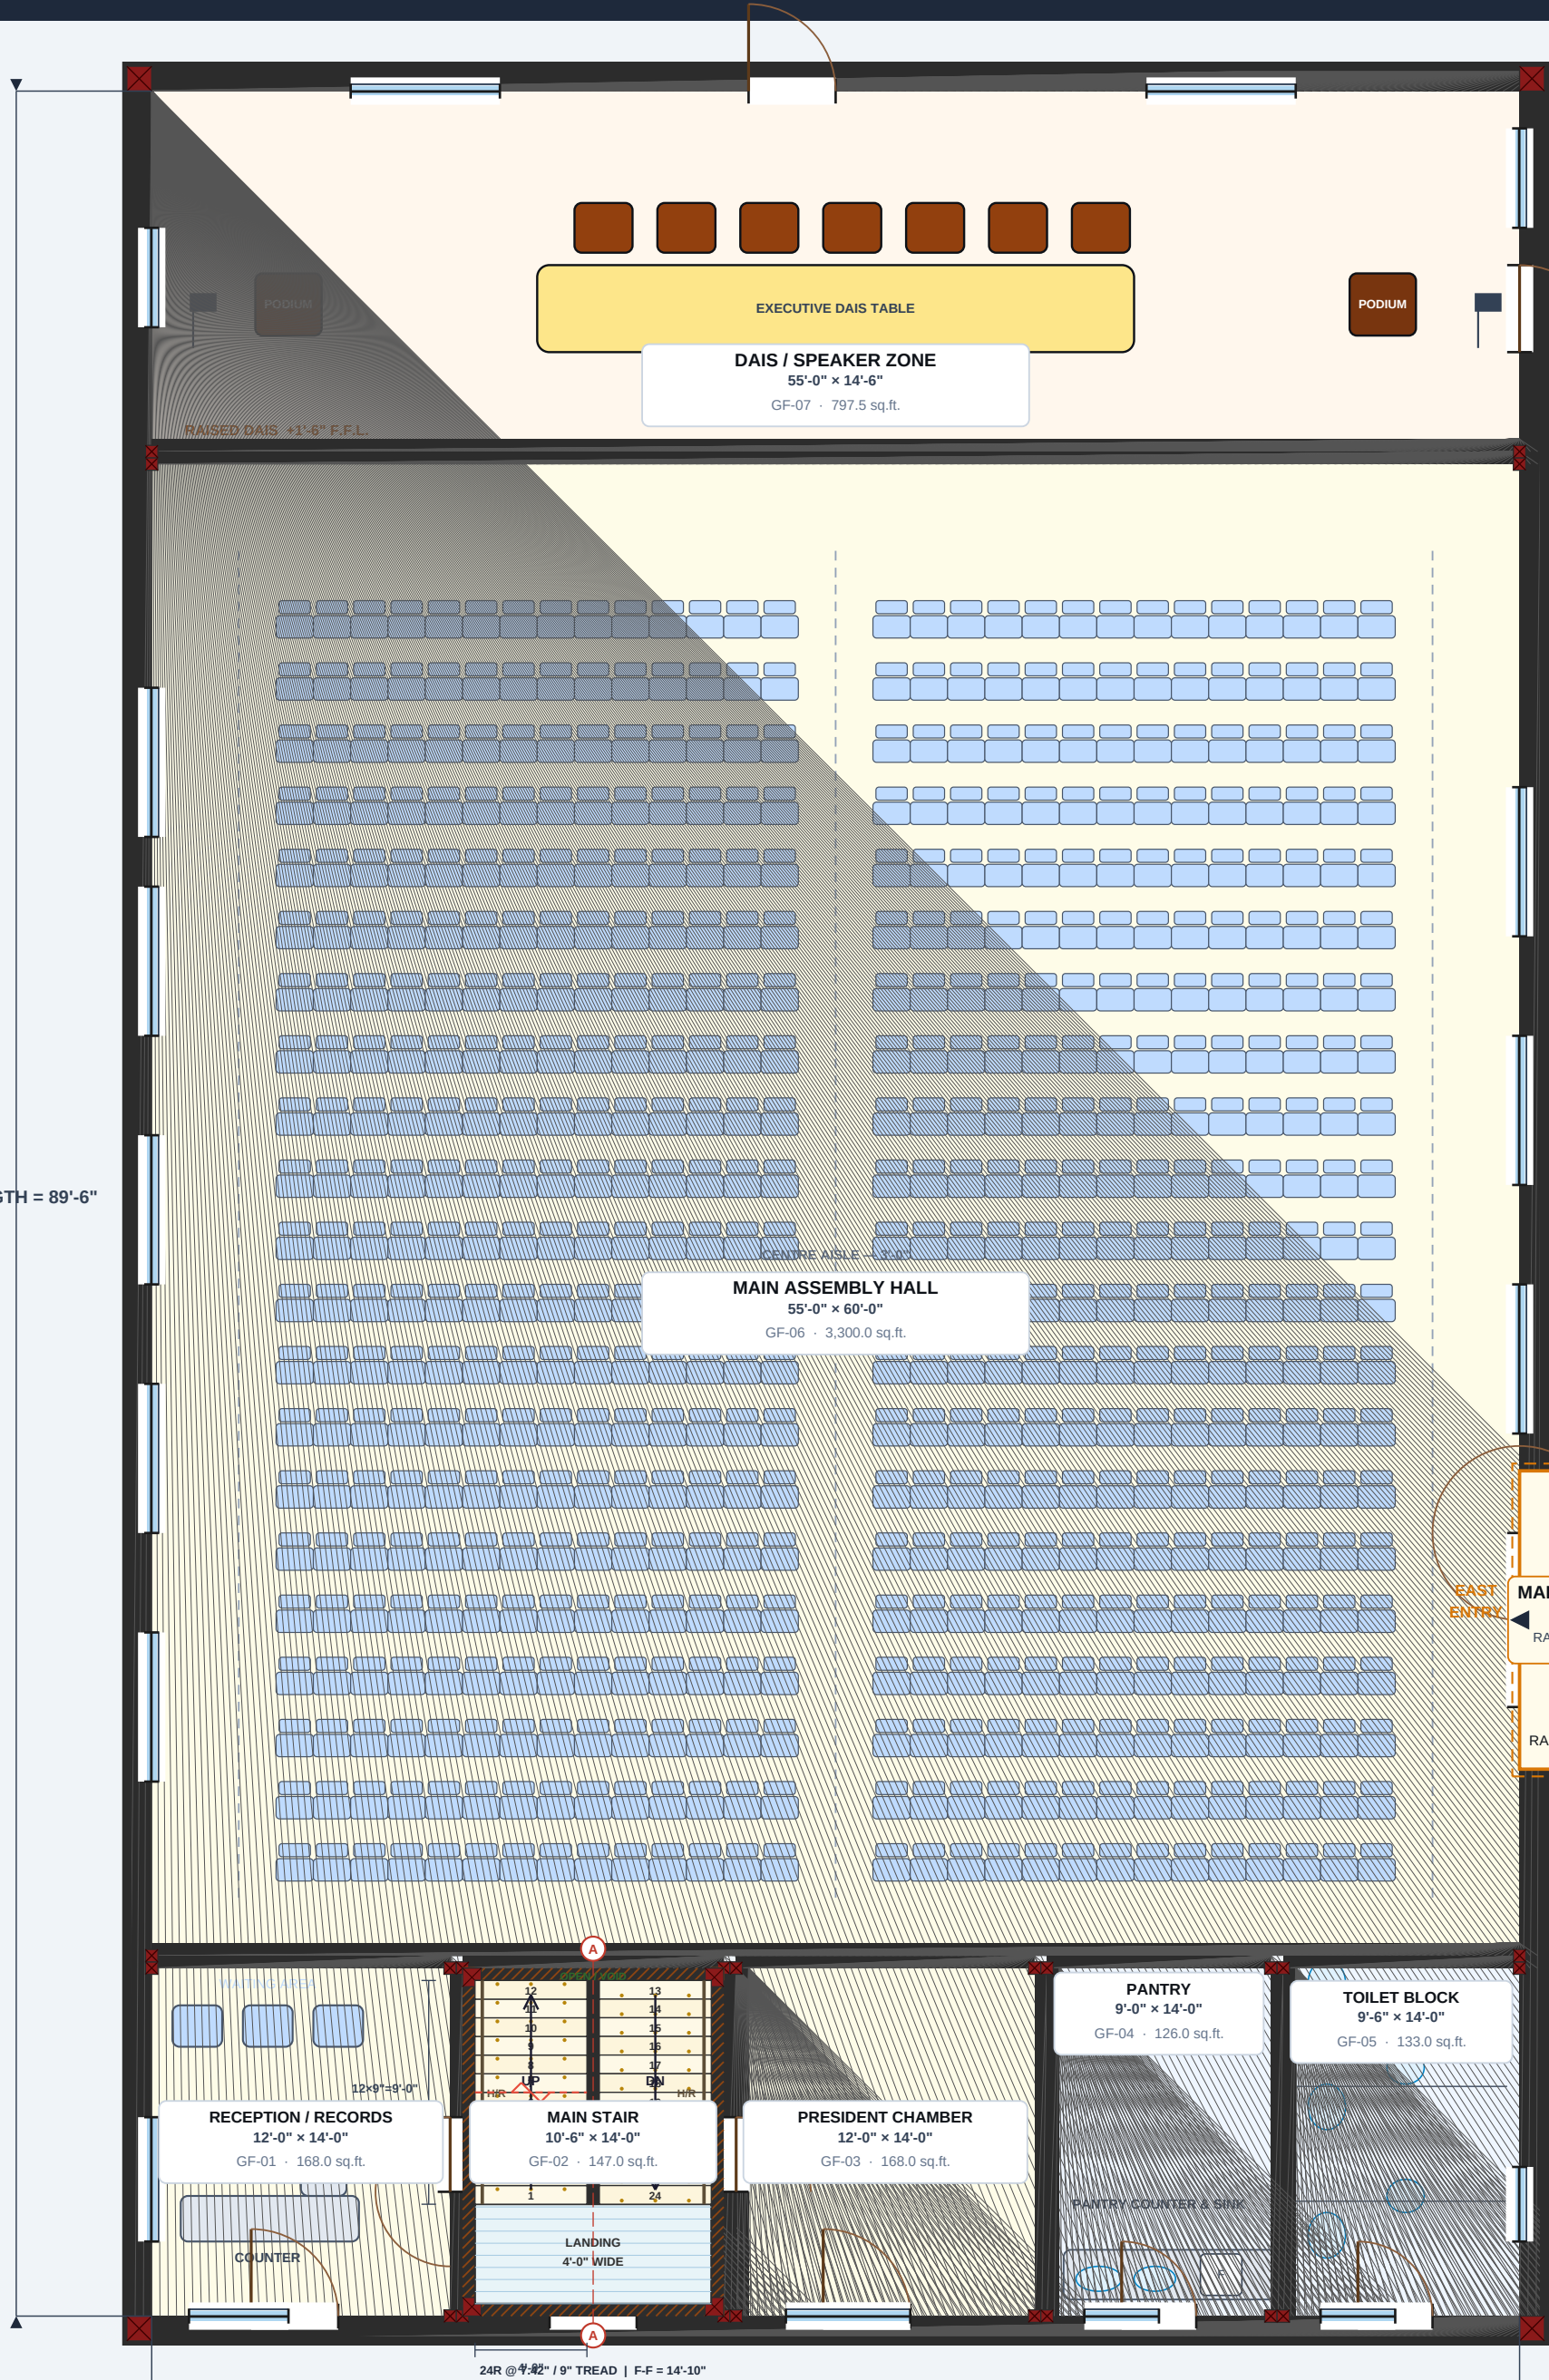

GRAPHIC SCALE 1/8" = 1'-0"



GENERAL NOTES & LEGEND

- Setback envelope: 4,427.50 sq ft per floor (site_plan.json).
- Main entrance EAST long wall, 12'-0"×8'-0" covered porch with ramp.
- Accessible ramp 1:12 slope and 5'-0" wide double-leaf entry door.
- Windows on all four facades (N,S,E,W) for cross-ventilation & daylight.
- Dog-leg stair: 18 risers @ 7.33" rise, 10" tread, mid-floor landing.
- RCC columns & beams per IS 456:2000. Seismic zone per IS 1893:2016.
- Survey boundary, fire NOC, local authority approval required before build.
- All dimensions shown are nominal planning dimensions ±25 mm.

CUT WALL DOOR/SWING WINDOW FURNITURE

ROOM / SPACE SCHEDULE

ID	SPACE NAME	SIZE
GF-01	Reception / Records	12'-0" × 14'-0"
GF-02	Main Stair	10'-6" × 14'-0"
GF-03	President Chamber	12'-0" × 14'-0"
GF-04	Pantry	9'-0" × 14'-0"
GF-05	Toilet Block	9'-6" × 14'-0"
GF-06	Main Assembly Hall	55'-0" × 60'-0"
TOTAL ADOPTABLE AREA		

BAR ASSOCIATION HALL
DISTRICT COURT COMPLEX, BANSWARA
RAJASTHAN, INDIA

PLANNING SETBACK ENVELOPE: 4,427.50 SQ.FT. PER FLOOR
MAIN ENTRY: EAST LONG WALL · WINDOWS: ALL FOUR SIDES

GROUND FLOOR PLAN

PRESENTATION FLOOR PLAN (WITH FURNITURE)

LEVEL: GROUND FLOOR SCALE: 1/8" = 1'-0" (A2 LANDSCAPE)

STRUCTURE: RCC FRAME IS 456:2000 / IS 1893:2016
STATUS: APPROVED SCHEMATIC — NOT FOR CONSTRUCTION

A-201


SHEET NO.

REV: P01
18-SEP-2026

S-101 | GROUND FLOOR PLAN

STRUCTURAL COLUMN & GRID COORDINATION PLAN (WITH COLUMNS)

BANSWARA DISTRICT COURT COMPLEX · COORDINATED ARCHITECTURAL SCHEMATIC

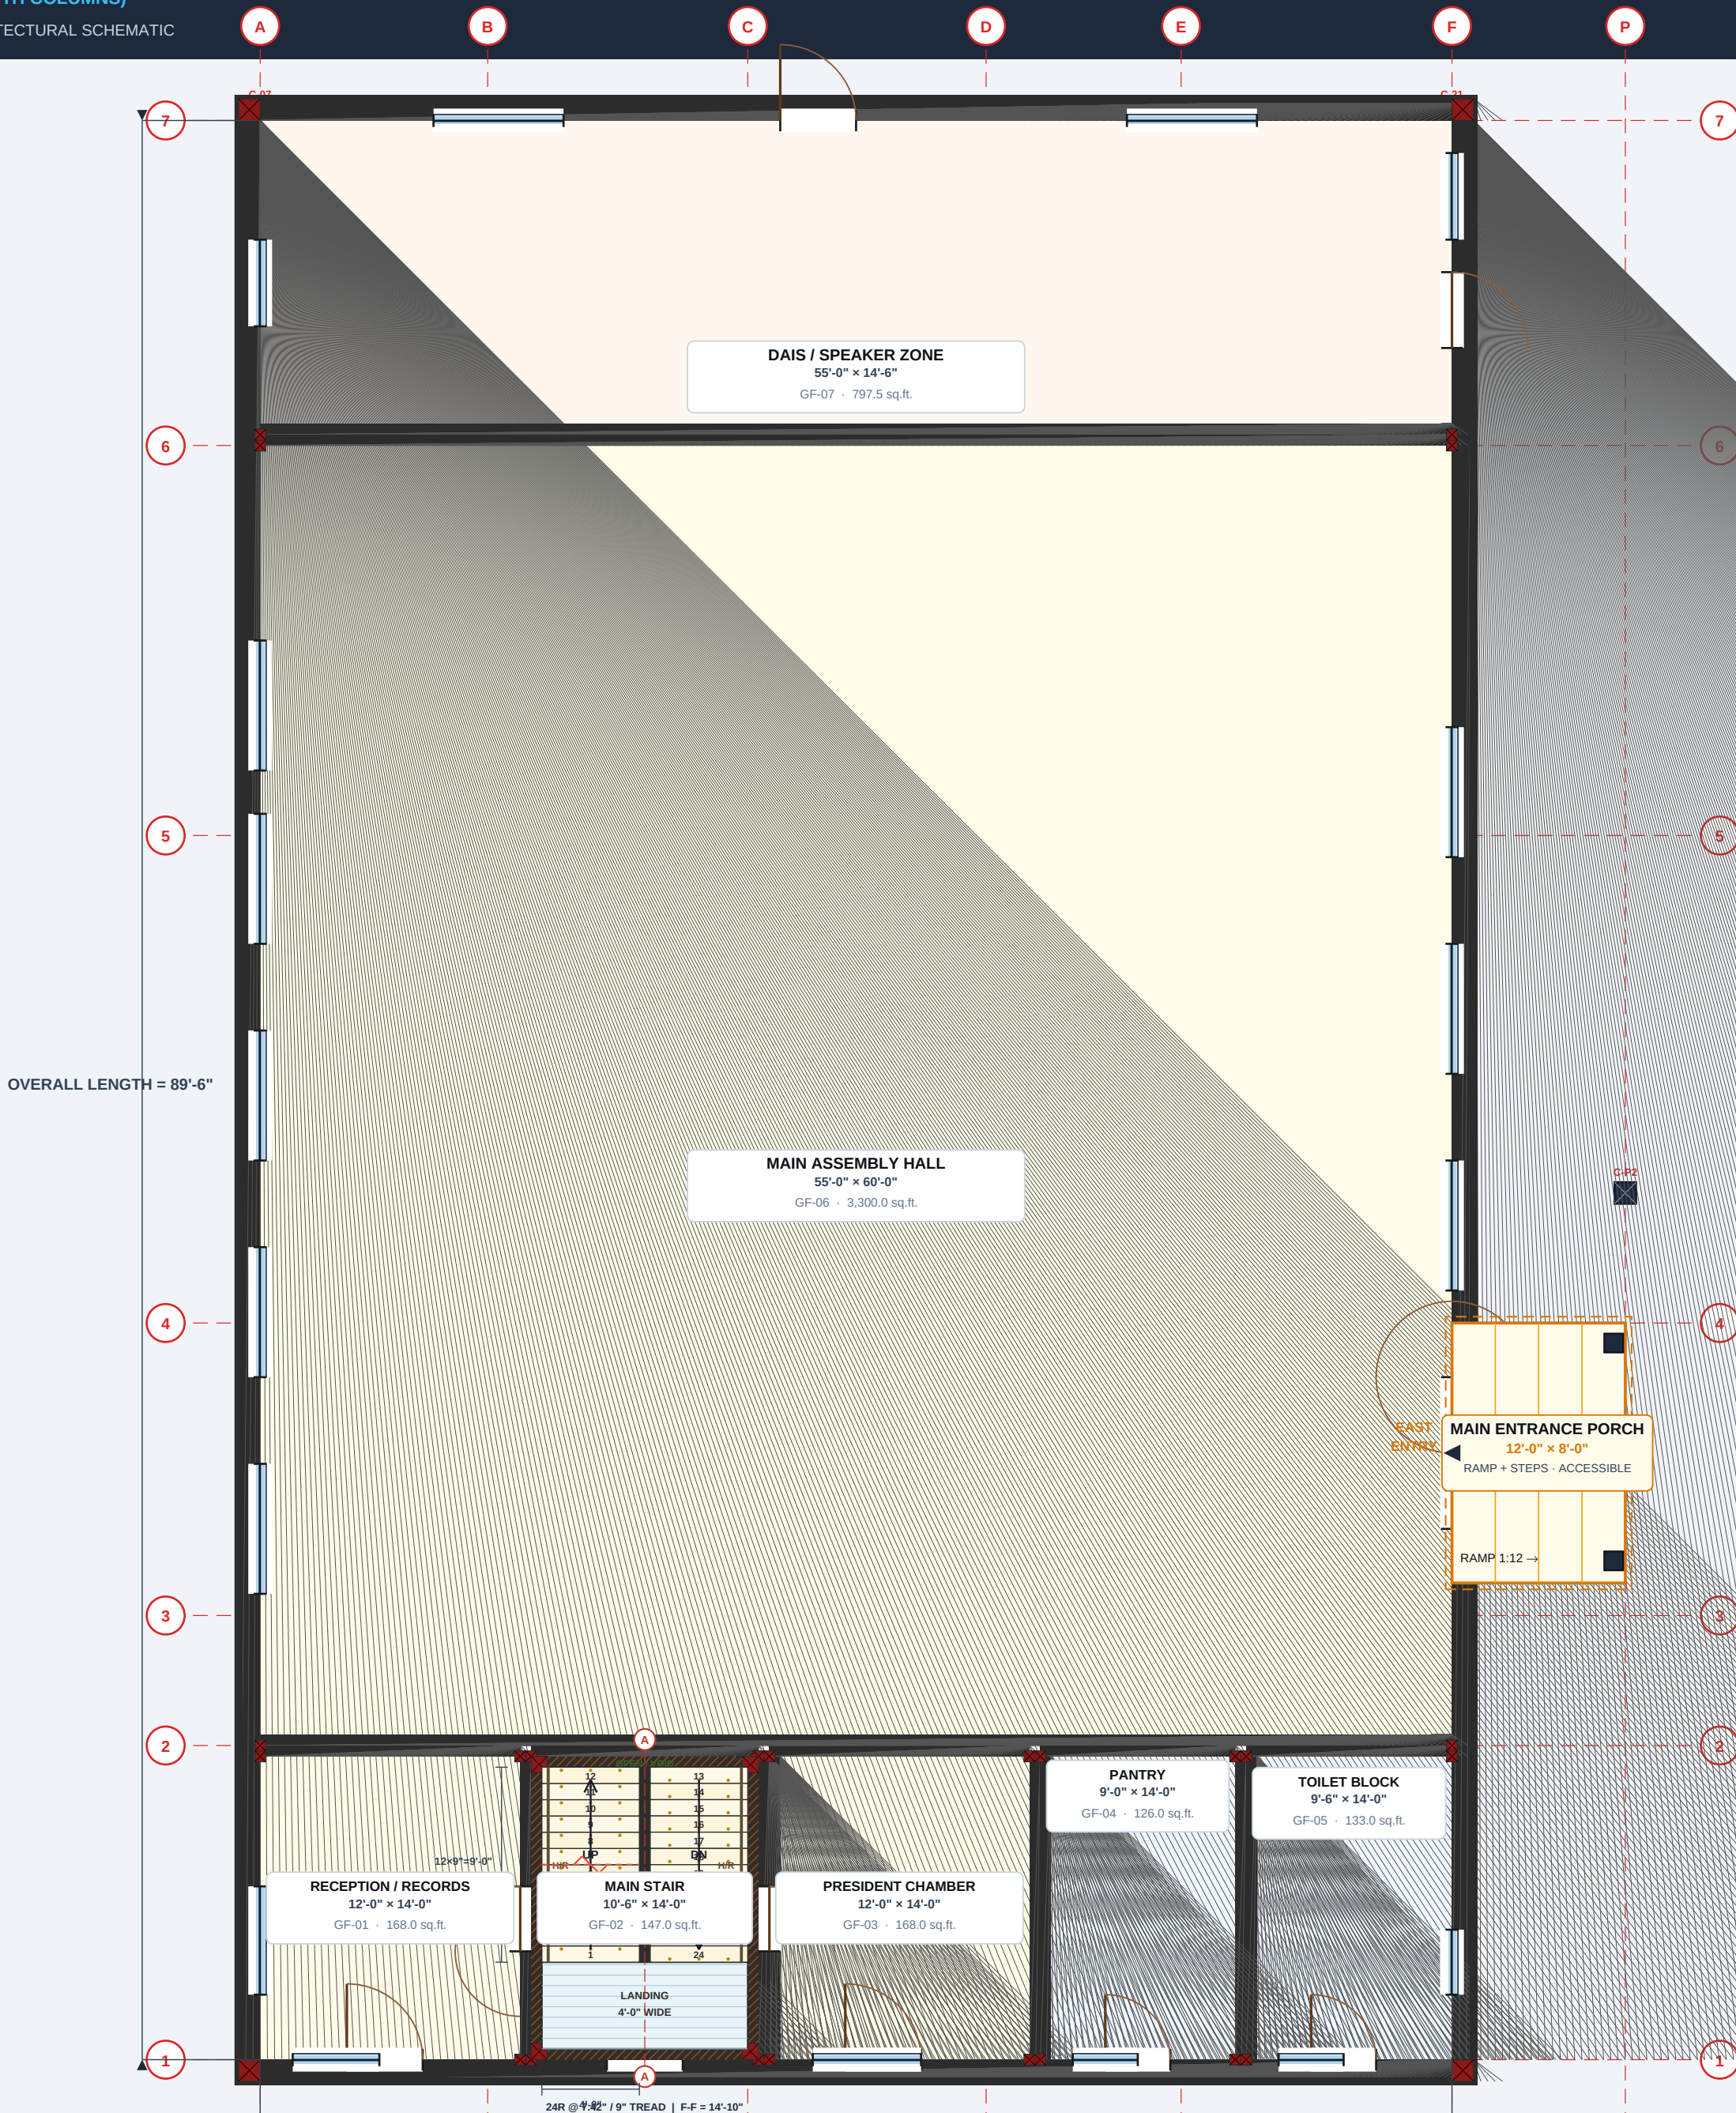

GRAPHIC SCALE 1/8" = 1'-0"

GENERAL NOTES & LEGEND

- Setback envelope: 4,427.50 sq ft per floor (site_plan.json).
- Main entrance EAST long wall, 12'-0"x8'-0" covered porch with ramp.
- Accessible ramp 1:12 slope and 5'-0" wide double-leaf entry door.
- Windows on all four facades (N,S,E,W) for cross-ventilation & daylight.
- Dog-leg stair: 18 risers @ 7.33" rise, 10" tread, mid-floor landing.
- RCC columns & beams per IS 456:2000. Seismic zone per IS 1893:2016.
- Survey boundary, fire NOC, local authority approval required before build.
- All dimensions shown are nominal planning dimensions ± 25 mm.

CUT WALL DOOR/SWING WINDOW RCC COLUMN

STRUCTURAL COLUMN SCHEDULE

MARK / SIZE	MAIN REBAR	ZONE
C1 - 300x600mm	8-T20+4-T16, Links T8@150	Main hall long-span perimeter
C2 - 300x450mm	8-T16, Links T8@150	Service core, stair, dais
CP - 300x300mm	4-T16, Links T8@150	Entrance porch canopy posts

M25 CONCRETE | Fe500D STEEL | ISOLATED RCC FOOTINGS

BAR ASSOCIATION HALL

DISTRICT COURT COMPLEX, BANSWARA

RAJASTHAN, INDIA

PLANNING SETBACK ENVELOPE: 4,427.50 SQ.FT. PER FLOOR

MAIN ENTRY: EAST LONG WALL · WINDOWS: ALL FOUR SIDES

GROUND FLOOR PLAN

STRUCTURAL COLUMN & GRID COORDINATION PLAN (WITH COLUMNS)

LEVEL: GROUND FLOOR SCALE: 1/8" = 1'-0" (A2 LANDSCAPE)

STRUCTURE: RCC FRAME IS 456:2000 / IS 1893:2016

STATUS: APPROVED SCHEMATIC — NOT FOR CONSTRUCTION

S-101

SHEET NO.


REV: P01

18-SEP-2026

A-102 | FIRST FLOOR PLAN

ARCHITECTURAL FLOOR PLAN (WITHOUT FURNITURE)

BANSWARA DISTRICT COURT COMPLEX · COORDINATED ARCHITECTURAL SCHEMATIC

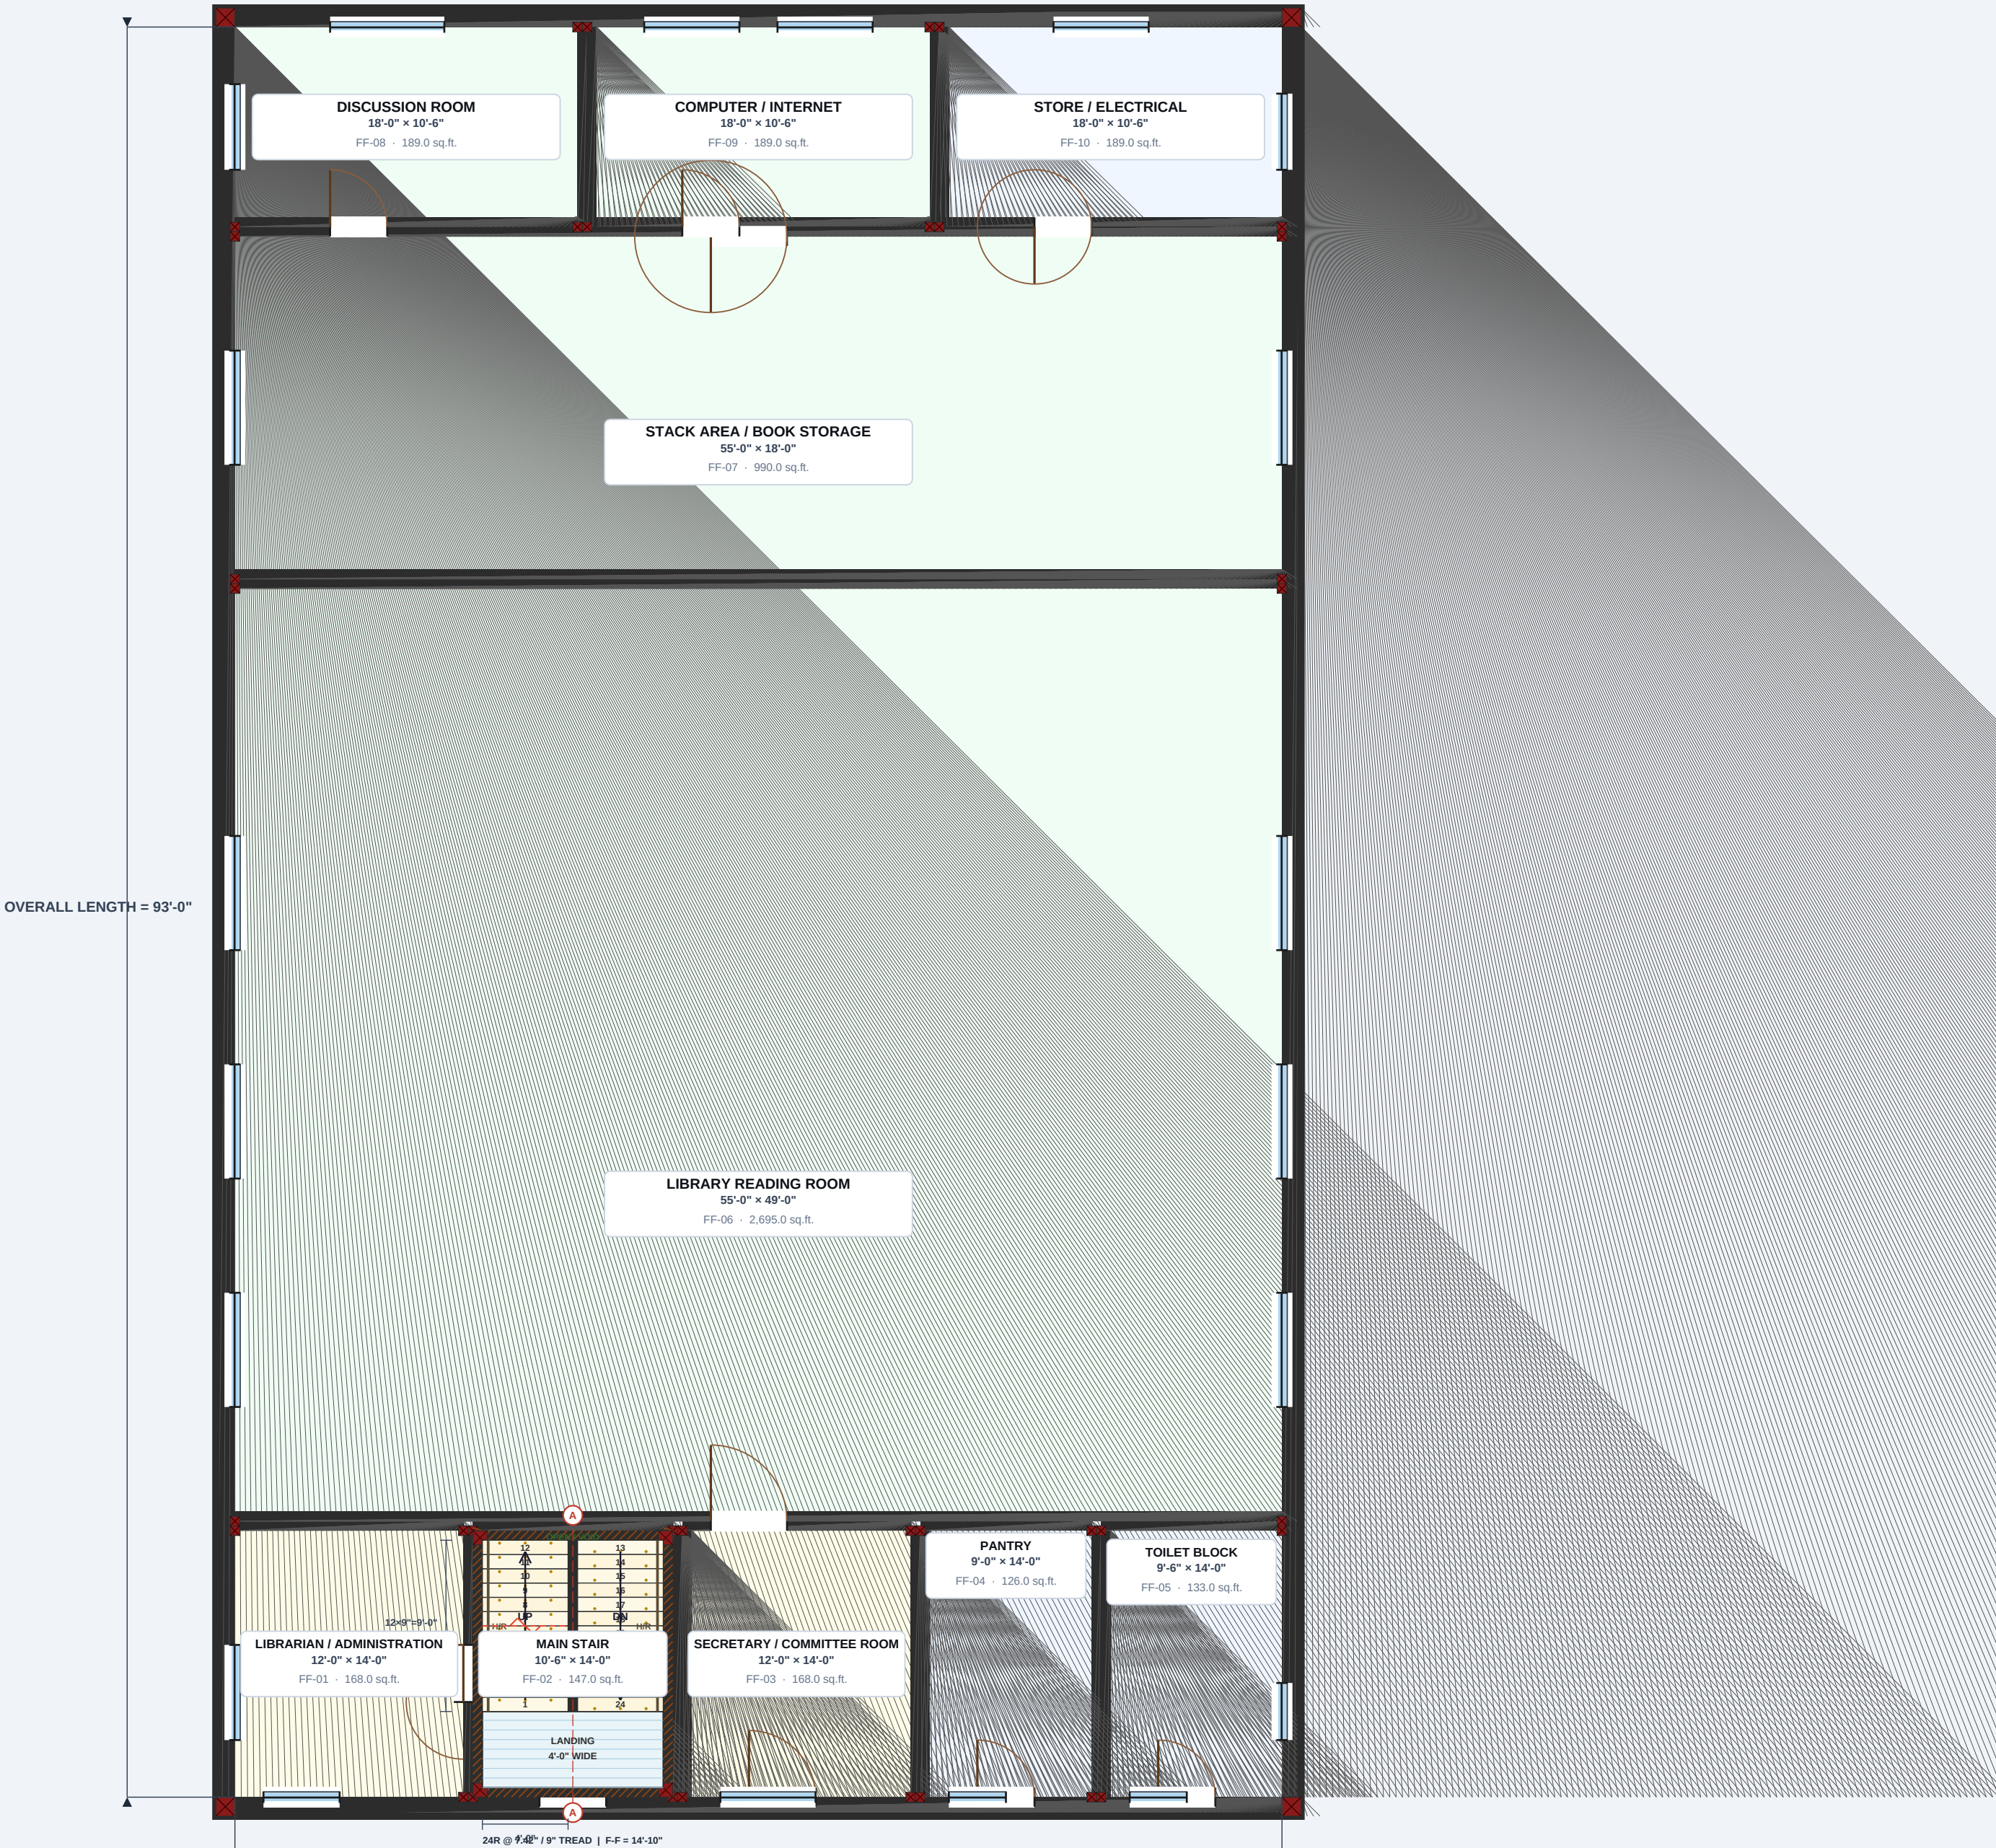

GRAPHIC SCALE 1/8" = 1'-0"



GENERAL NOTES & LEGEND

- Setback envelope: 4,427.50 sq ft per floor (site_plan.json).
- Main entrance EAST long wall, 12'-0"×8'-0" covered porch with ramp.
- Accessible ramp 1:12 slope and 5'-0" wide double-leaf entry door.
- Windows on all four facades (N,S,E,W) for cross-ventilation & daylight.
- Dog-leg stair: 18 risers @ 7.33" rise, 10" tread, mid-floor landing.
- RCC columns & beams per IS 456:2000. Seismic zone per IS 1893:2016.
- Survey boundary, fire NOC, local authority approval required before build.
- All dimensions shown are nominal planning dimensions ±25 mm.

CUT WALL DOOR/SWING WINDOW

ROOM / SPACE SCHEDULE

ID	SPACE NAME	SIZE
FF-01	Librarian / Administration	12'-0" × 14'-0"
FF-02	Main Stair	10'-6" × 14'-0"
FF-03	Secretary / Committee Room	12'-0" × 14'-0"
FF-04	Pantry	9'-0" × 14'-0"
FF-05	Toilet Block	9'-6" × 14'-0"
FF-06	Library Reading Room	55'-0" × 49'-0"
FF-07	Stack Area / Book Storage	55'-0" × 18'-0"
FF-08	Discussion Room	18'-0" × 10'-6"
FF-09	Computer / Internet	18'-0" × 10'-6"
TOTAL ADOPTABLE AREA		

BAR ASSOCIATION HALL
DISTRICT COURT COMPLEX, BANSWARA
RAJASTHAN, INDIA

PLANNING SETBACK ENVELOPE: 4,427.50 SQ.FT. PER FLOOR
MAIN ENTRY: EAST LONG WALL · WINDOWS: ALL FOUR SIDES

FIRST FLOOR PLAN
ARCHITECTURAL FLOOR PLAN (WITHOUT FURNITURE)
LEVEL: FIRST FLOOR SCALE: 1/8" = 1'-0" (A2 LANDSCAPE)

STRUCTURE: RCC FRAME IS 456:2000 / IS 1893:2016
STATUS: APPROVED SCHEMATIC — NOT FOR CONSTRUCTION

A-102


SHEET NO.

REV: P01
18-SEP-2026

A-202 | FIRST FLOOR PLAN

PRESENTATION FLOOR PLAN (WITH FURNITURE)

BANSWARA DISTRICT COURT COMPLEX · COORDINATED ARCHITECTURAL SCHEMATIC

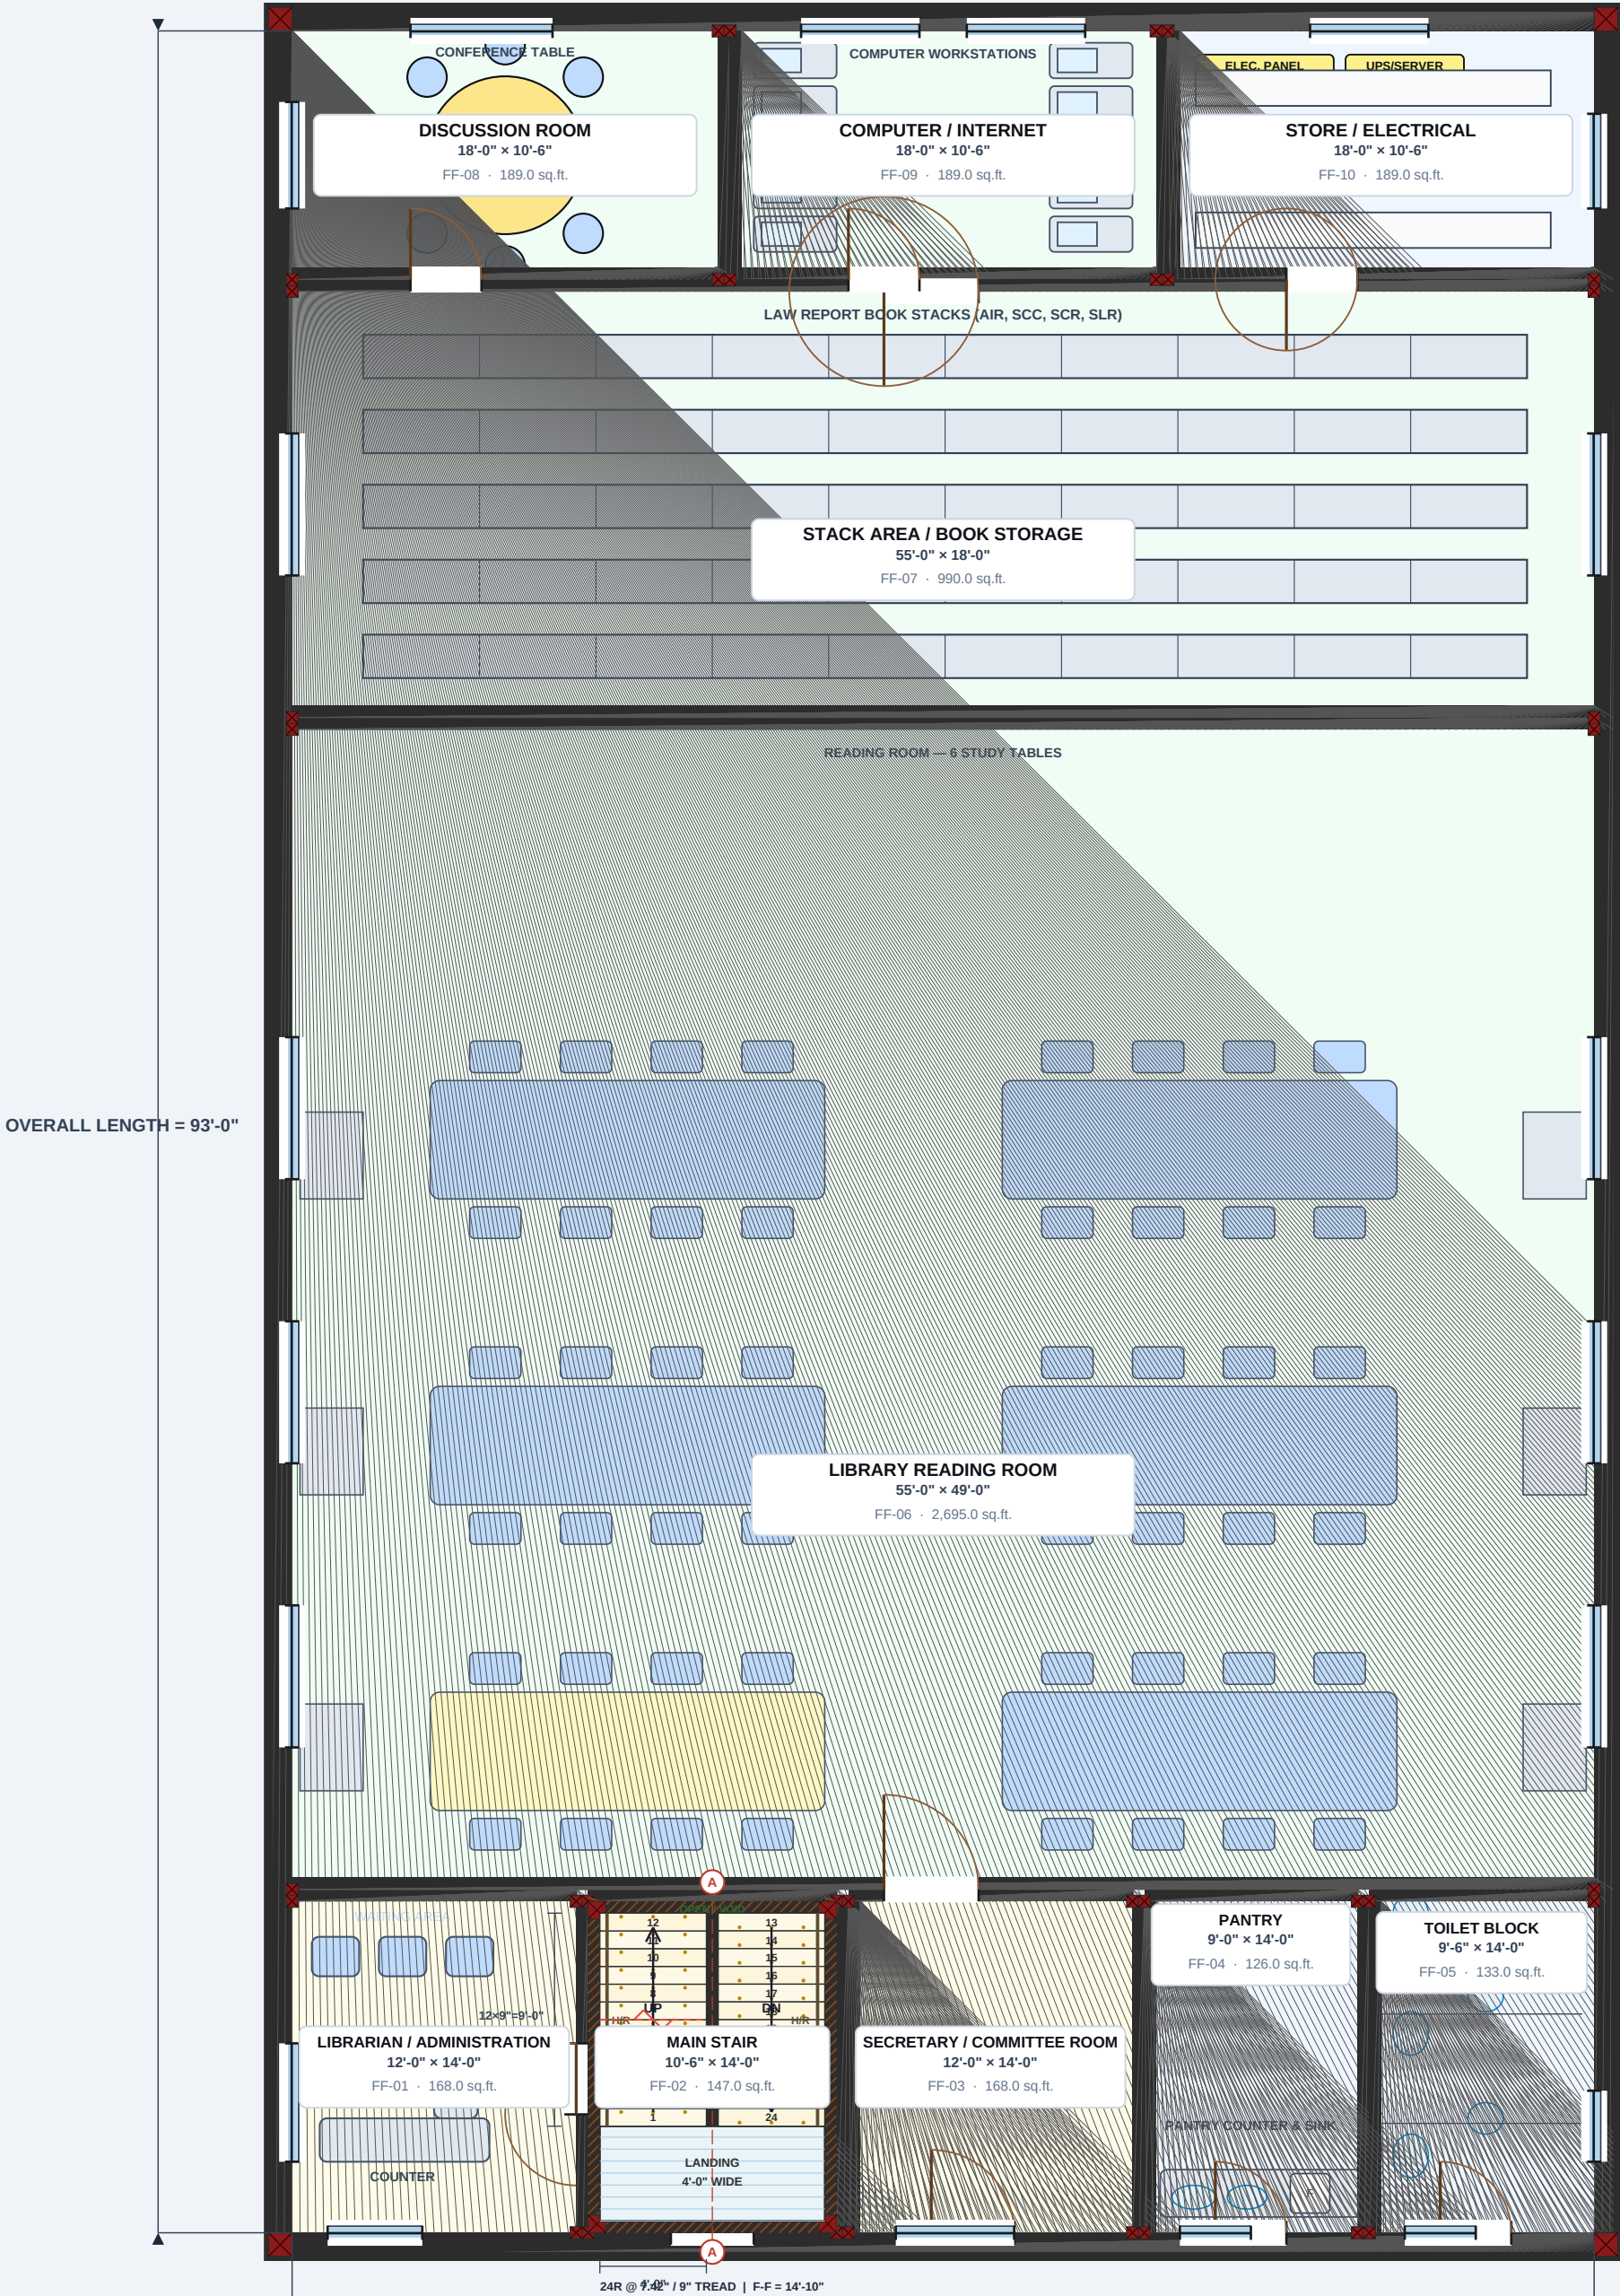

GRAPHIC SCALE 1/8" = 1'-0"



GENERAL NOTES & LEGEND

- Setback envelope: 4,427.50 sq ft per floor (site_plan.json).
- Main entrance EAST long wall, 12'-0"×8'-0" covered porch with ramp.
- Accessible ramp 1:12 slope and 5'-0" wide double-leaf entry door.
- Windows on all four facades (N,S,E,W) for cross-ventilation & daylight.
- Dog-leg stair: 18 risers @ 7.33" rise, 10" tread, mid-floor landing.
- RCC columns & beams per IS 456:2000. Seismic zone per IS 1893:2016.
- Survey boundary, fire NOC, local authority approval required before build.
- All dimensions shown are nominal planning dimensions ±25 mm.

CUT WALL DOOR/SWING WINDOW FURNITURE

BAR ASSOCIATION HALL
DISTRICT COURT COMPLEX, BANSWARA
RAJASTHAN, INDIA

PLANNING SETBACK ENVELOPE: 4,427.50 SQ.FT. PER FLOOR
MAIN ENTRY: EAST LONG WALL · WINDOWS: ALL FOUR SIDES

FIRST FLOOR PLAN
PRESENTATION FLOOR PLAN (WITH FURNITURE)
LEVEL: FIRST FLOOR SCALE: 1/8" = 1'-0" (A2 LANDSCAPE)

STRUCTURE: RCC FRAME IS 456:2000 / IS 1893:2016
STATUS: APPROVED SCHEMATIC — NOT FOR CONSTRUCTION

A-202


SHEET NO.

REV: P01
18-SEP-2026

S-102 | FIRST FLOOR PLAN

STRUCTURAL COLUMN & GRID COORDINATION PLAN (WITH COLUMNS)

BANSWARA DISTRICT COURT COMPLEX · COORDINATED ARCHITECTURAL SCHEMATIC

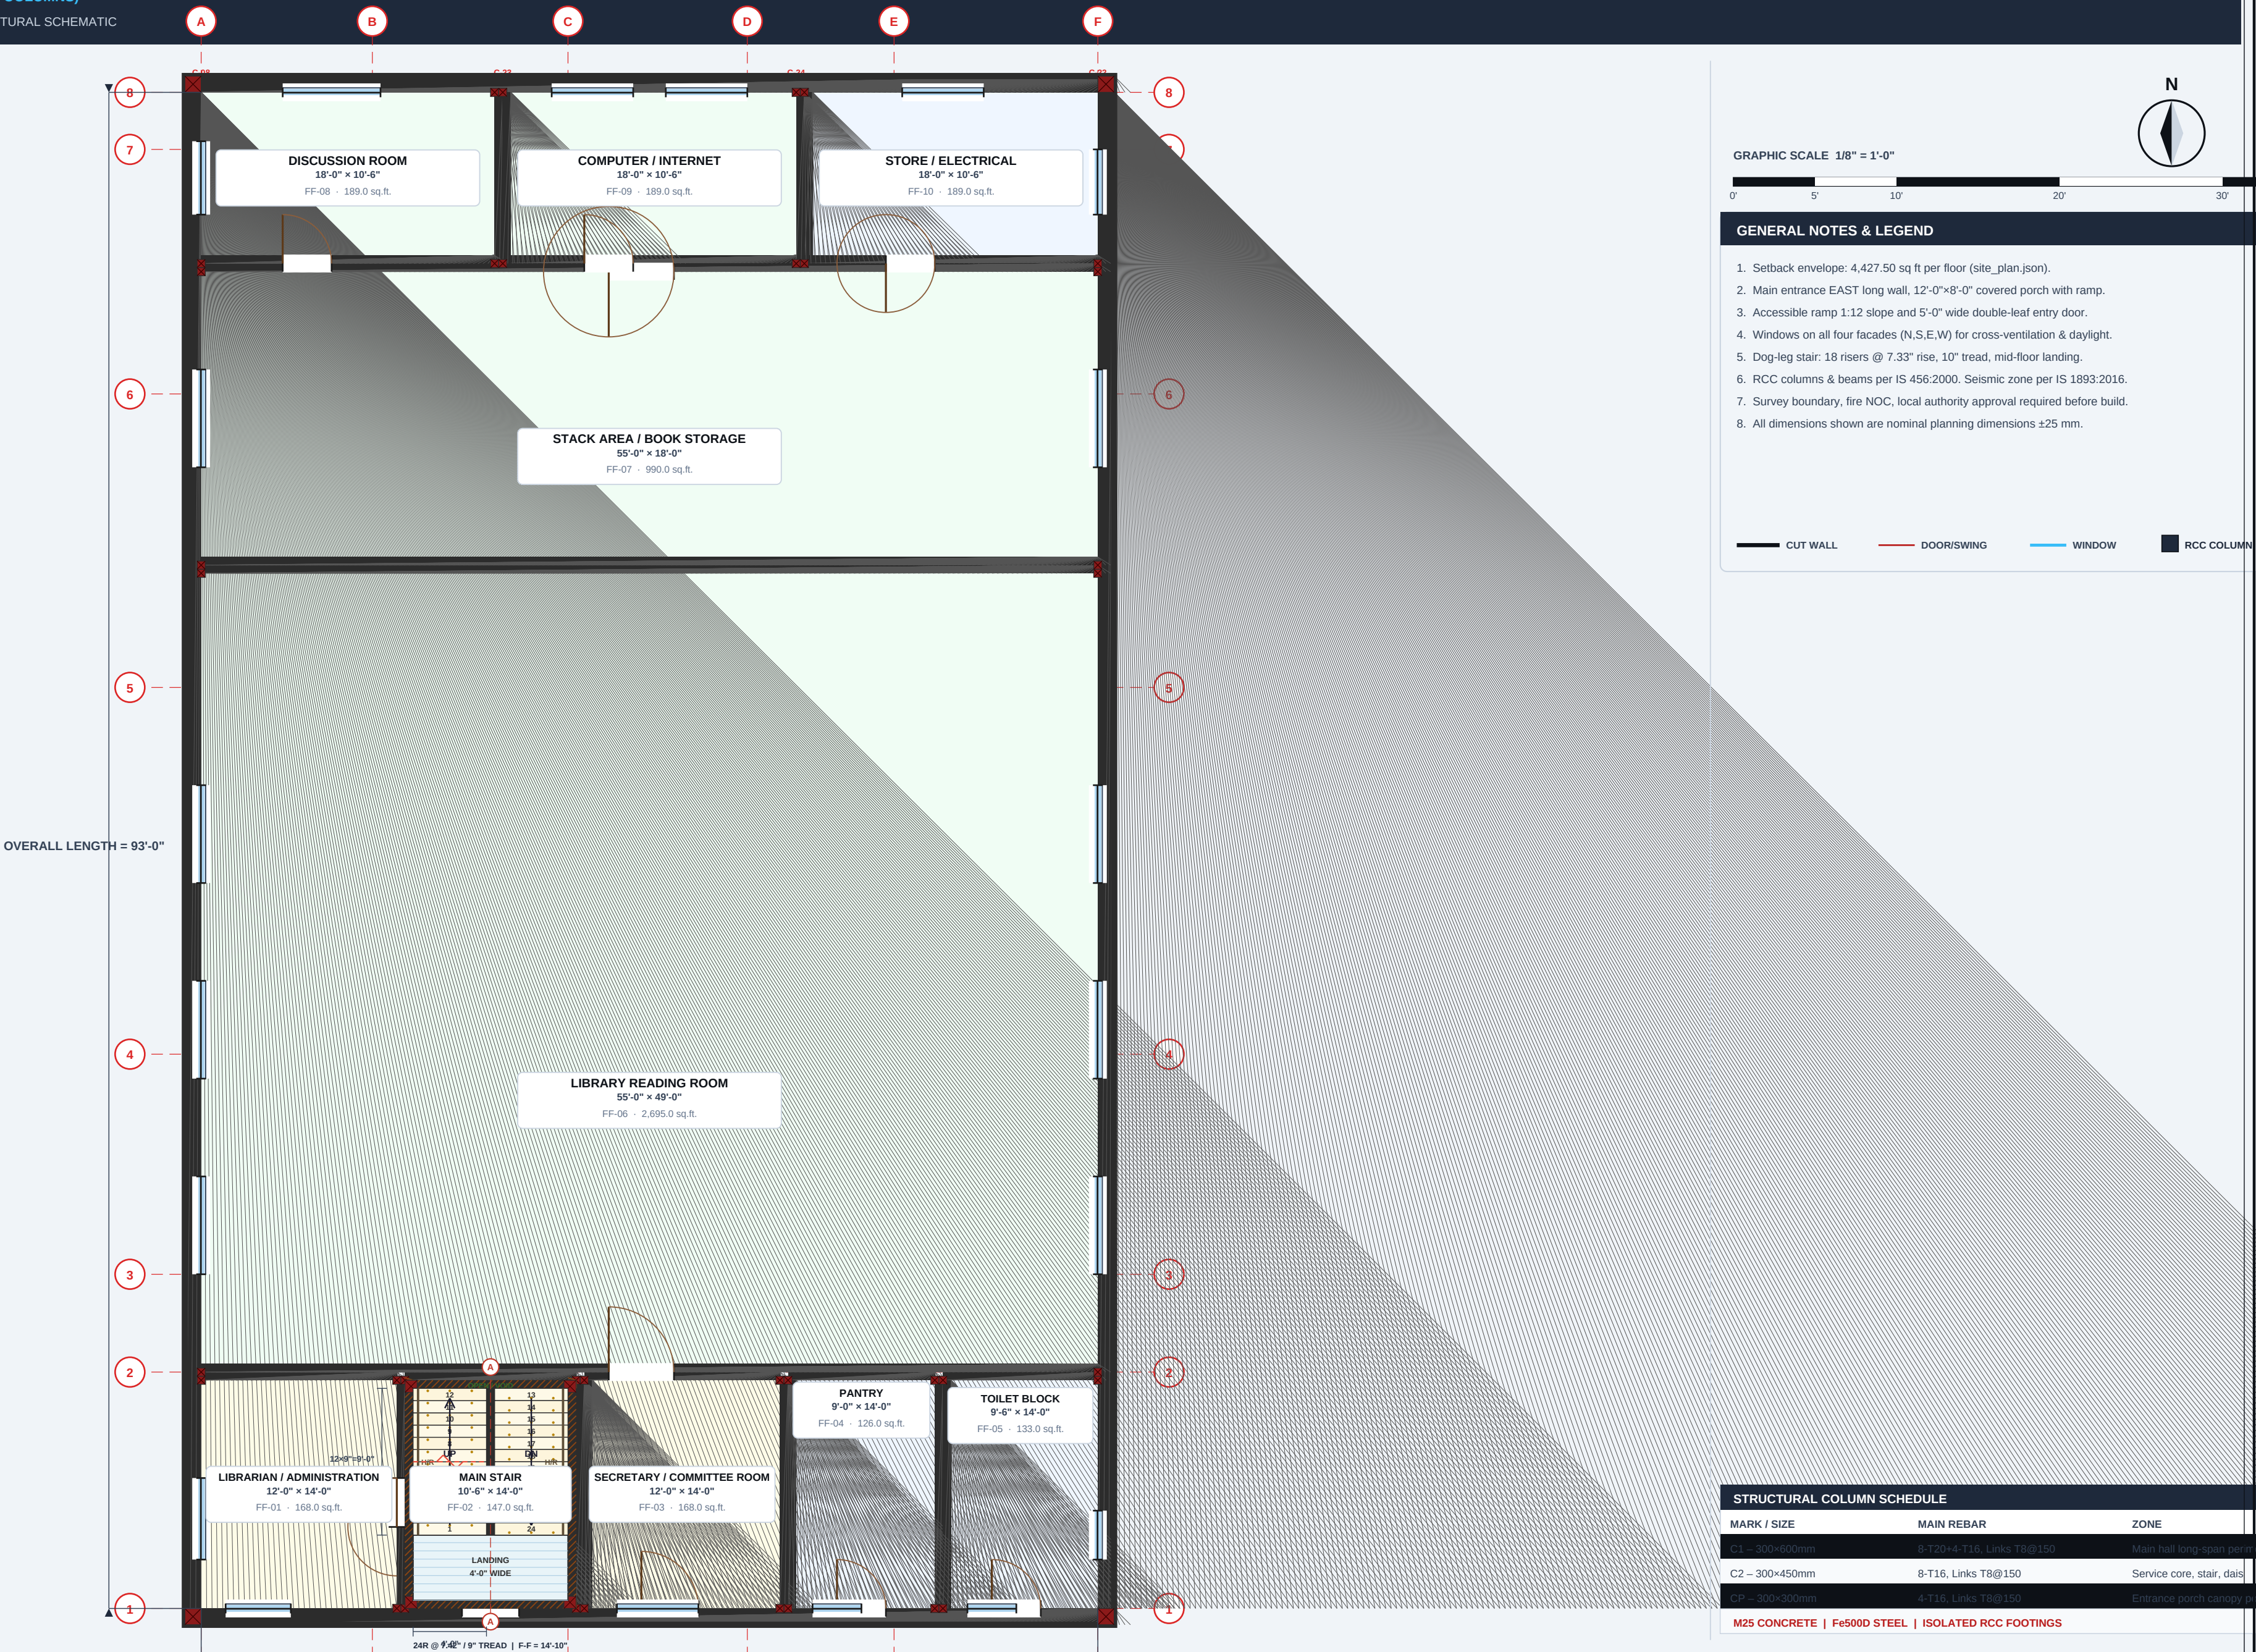

BAR ASSOCIATION HALL
DISTRICT COURT COMPLEX, BANSWARA
RAJASTHAN, INDIA

PLANNING SETBACK ENVELOPE: 4,427.50 SQ.FT. PER FLOOR
MAIN ENTRY: EAST LONG WALL · WINDOWS: ALL FOUR SIDES

FIRST FLOOR PLAN
STRUCTURAL COLUMN & GRID COORDINATION PLAN (WITH COLUMNS)
LEVEL: FIRST FLOOR SCALE: 1/8" = 1'-0" (A2 LANDSCAPE)

STRUCTURE: RCC FRAME IS 456:2000 / IS 1893:2016
STATUS: APPROVED SCHEMATIC — NOT FOR CONSTRUCTION

S-102

SHEET NO.

REV: P01
18-SEP-2026