


S-101 | GROUND FLOOR PLAN

STRUCTURAL COLUMN & GRID COORDINATION PLAN (WITH COLUMNS)

BANSWARA DISTRICT COURT COMPLEX · COORDINATED ARCHITECTURAL SCHEMATIC

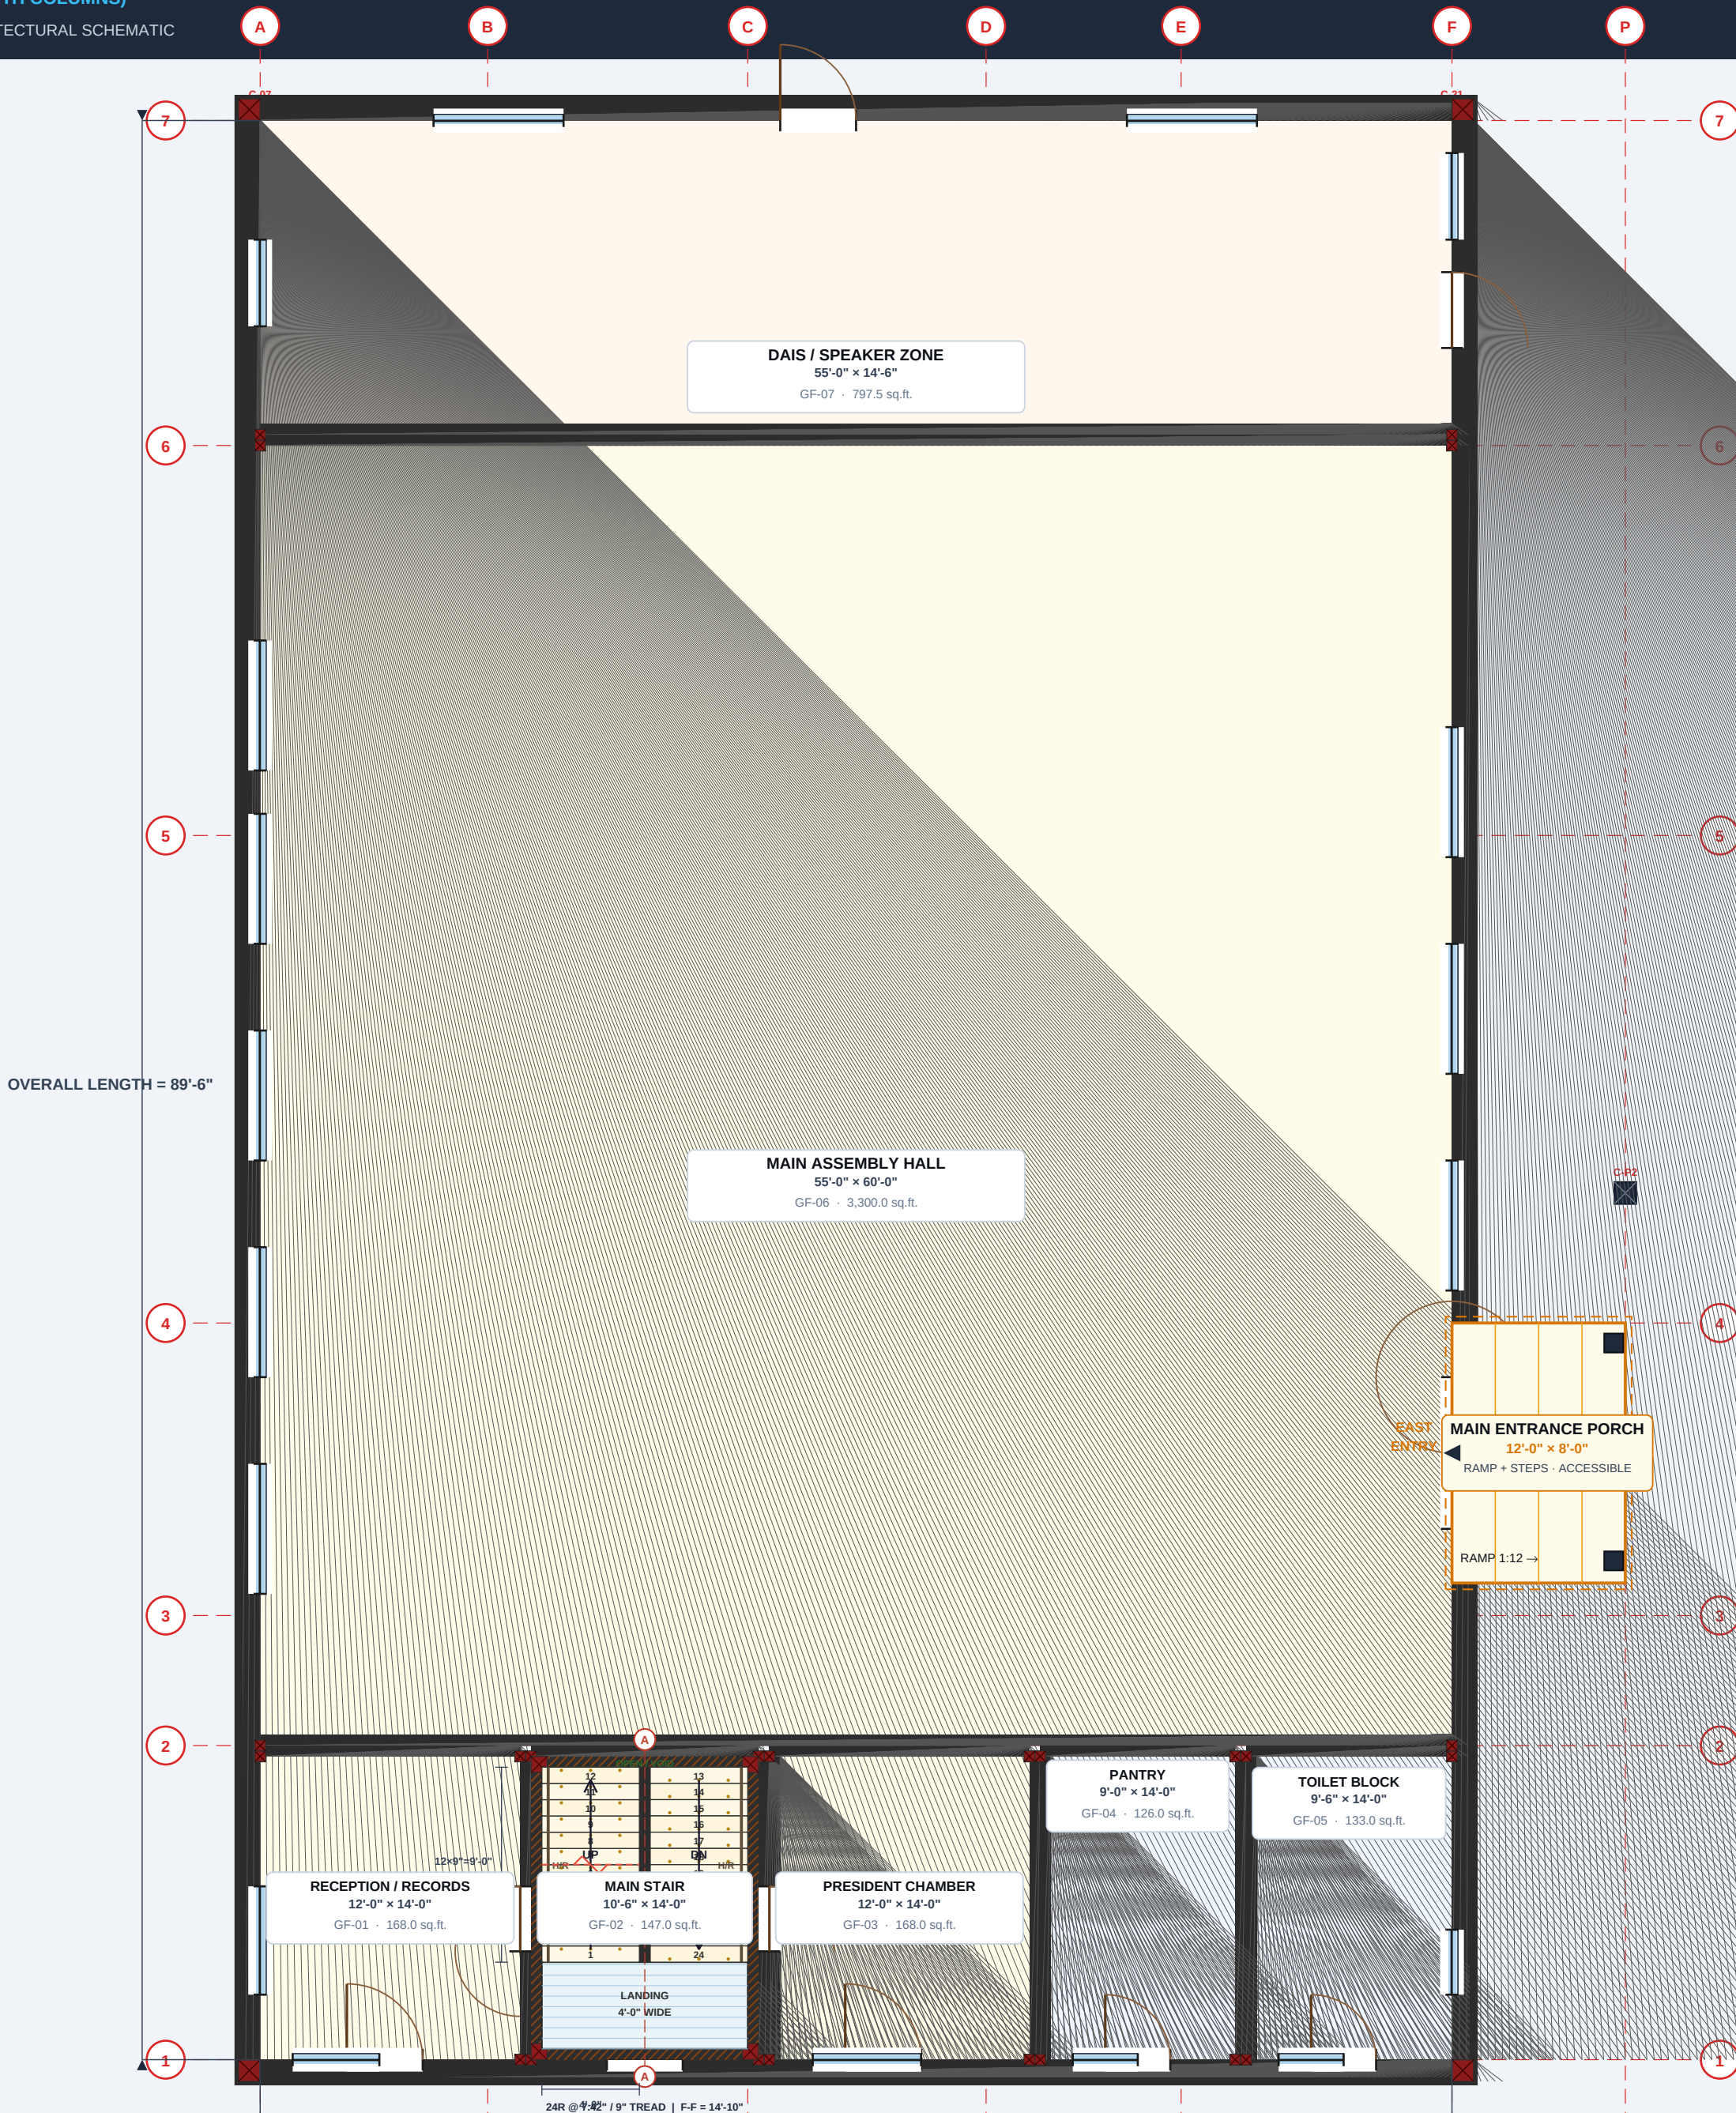

GRAPHIC SCALE 1/8" = 1'-0"

0' 5' 10' 20' 30'

GENERAL NOTES & LEGEND

- Setback envelope: 4,427.50 sq ft per floor (site_plan.json).
- Main entrance EAST long wall, 12'-0"x8'-0" covered porch with ramp.
- Accessible ramp 1:12 slope and 5'-0" wide double-leaf entry door.
- Windows on all four facades (N,S,E,W) for cross-ventilation & daylight.
- Dog-leg stair: 18 risers @ 7.33" rise, 10" tread, mid-floor landing.
- RCC columns & beams per IS 456:2000. Seismic zone per IS 1893:2016.
- Survey boundary, fire NOC, local authority approval required before build.
- All dimensions shown are nominal planning dimensions ± 25 mm.

CUT WALL DOOR/SWING WINDOW RCC COLUMN

STRUCTURAL COLUMN SCHEDULE

MARK / SIZE	MAIN REBAR	ZONE
C1 - 300x600mm	8-T20+4-T16, Links T8@150	Main hall long-span perimeter
C2 - 300x450mm	8-T16, Links T8@150	Service core, stair, dais
CP - 300x300mm	4-T16, Links T8@150	Entrance porch canopy posts

M25 CONCRETE | Fe500D STEEL | ISOLATED RCC FOOTINGS

BAR ASSOCIATION HALL
DISTRICT COURT COMPLEX, BANSWARA
RAJASTHAN, INDIA

PLANNING SETBACK ENVELOPE: 4,427.50 SQ.FT. PER FLOOR
MAIN ENTRY: EAST LONG WALL · WINDOWS: ALL FOUR SIDES

GROUND FLOOR PLAN
STRUCTURAL COLUMN & GRID COORDINATION PLAN (WITH COLUMNS)
LEVEL: GROUND FLOOR SCALE: 1/8" = 1'-0" (A2 LANDSCAPE)

STRUCTURE: RCC FRAME IS 456:2000 / IS 1893:2016
STATUS: APPROVED SCHEMATIC — NOT FOR CONSTRUCTION

S-101

SHEET NO.

REV: P01
18-SEP-2026